


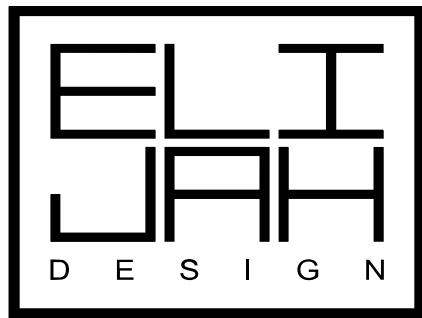


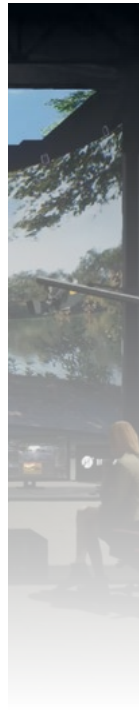

www.elijah-design.com

PORTFOLIO

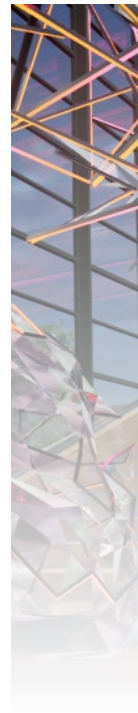

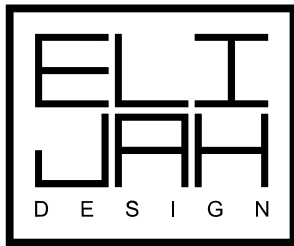

ELIJAH ALEJANDRO


 <https://www.linkedin.com/in/elijah-design>
 designs.elijah@gmail.com

www.elijah-design.com



TECHNICAL SKILLS


ARCHITECTURE PROGRAMS

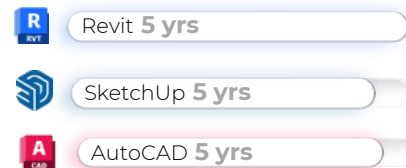

RENDERING PROGRAMS



ADOBE PROGRAMS

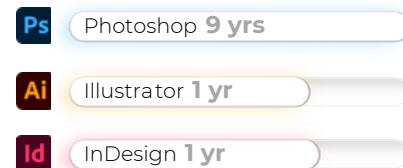

PROFESSIONAL EXPERIENCE SUMMARY

Interior designer with experience in **space planning, custom millwork drawings**, and the production of **coordinated construction drawing sets**. Strong technical background in **Revit**, including **family creation, troubleshooting**, and **team support**. Experienced in **material and FFE sourcing, client and supplier coordination**, and maintaining clear **project documentation**. Known for creating thoughtful, **story-driven presentations** across **digital and physical formats**.

AWARDS & RECOGNITION

- Graduate with Honours 2024 at Humber College
- [VR Digital Twin Cameras](#) - A VR Learning Extension App 2024 (Humber College Academic Plan [Priority 3 Project](#))
- Women in STEM (2023 NSERC funded [research collaboration](#) between [Humber College](#) and [APG Media](#))
- [Harnessing the Metaverse in Higher Education](#) (Interdisciplinary Collaboration 2023)
- Recipient of [Humber College Winter 2022 Pizzale Design Award](#) for [Restaurant Hospitality Project](#)

VAN DER KING DESIGN GROUP INC.

Junior Designer – Hybrid | 1yr | 2024 – 2025



- Designed custom wallcoverings and client-themed logos
- Generated detailed Revit sets: plans, sections, elevations, power layouts
- Created Revit parameters/tags for millwork and finishes
- Coordinated in-person and virtual presentations with suppliers and design teams
- Provided Revit and Photoshop training to colleagues

II BY IV DESIGN GROUP INC.

Design Intern – In-person | 1yr | 2022-2023



- Created client presentations using Photoshop to communicate design concepts.
- Organized and maintained the material library, assisting designers in collaborating with suppliers.
- Sourced material finishes from supplier lists and coordinated with specialists.
- Prepared and organized millwork drawings for project implementation.
- Contributed to floor plan adjustments and space planning in Revit, AutoCAD, SketchUp, and Layout.
- Developed 3D models based on schematic design concepts

TRUONG LY DESIGN INC.

Design Intern – Online | 1yr | 2021-2022



- Prepared and organized millwork drawings and custom light fixture designs.
- Built 3D models and adjusted floor plans based on schematic designs using Revit, AutoCAD, SketchUp, and Layout.
- Assisted in the schematic design and design development phases.
- Assisted in developing a design proposal for a showroom project bid.
- Provided team training on rendering techniques in Enscape.
- Supported space planning and layout coordination.

MULTIDISCIPLINARY DESIGNER

Freelance | 4yr | 2022 – Present



- Utilized Photoshop to create client presentations, posters, and visual materials.
- Edited and updated website content to enhance educational program visibility.
- Collaborated with interdisciplinary teams on innovative VR and Metaverse projects.
- Supported research initiatives, including NSERC-funded Women in STEM projects.
- Contributed to the design of logos, software, UX/UI elements, and website development.

TABLE OF CONTENTS

COMMERCIAL



SPORTS | RETAIL



HOSPITALITY | RESTAURANT + BAR



RETAIL | SALES CENTRE



HOSPITALITY | FINE DINING RESTAURANT

RESIDENTIAL



SENIOR LIVING | WELLNESS CENTRE



VERTICAL LIVING | LOFT

PASSION PROJECT



METaverse | VIRTUAL REALITY



METaverse | VIRTUAL REALITY



2024 RINGFIT

BOXING GYM

SKETCHUP + TWINMOTION

CLIENT

Stephan Boyd | Lower Level, 1 St Clair Ave E Unit B002,
Toronto, ON M4T 2V7

Founded in 2008 by Stephan Boyd—a Canadian Middleweight Champion and former national team member for both Canada and Jamaica—RingFit brings 20 years of boxing and coaching experience into a newly designed studio. Stephan's inclusive approach welcomes all ages, body types, and experience levels. The interior reflects this vision through a **modern industrial aesthetic** with raw finishes, exposed structure, and open zones dedicated to serious training. The space is purpose-built to inspire focus, movement, and growth.




FROM CONCEPT TO BUILD


This was my first solo project, completed from initial design concept through project completion. Ontario Building Code (OBC) requirements were applied strategically to maximize usable space in response to client needs.

The work received positive feedback from the building's architect and engineer. I sourced FFE and coordinated with custom fabricators to ensure boxing equipment met safety and performance requirements, while maintaining alignment with the project budget.


COLUMNS WRAPPED IN DISTRESSED MATTE BLACK LEATHER

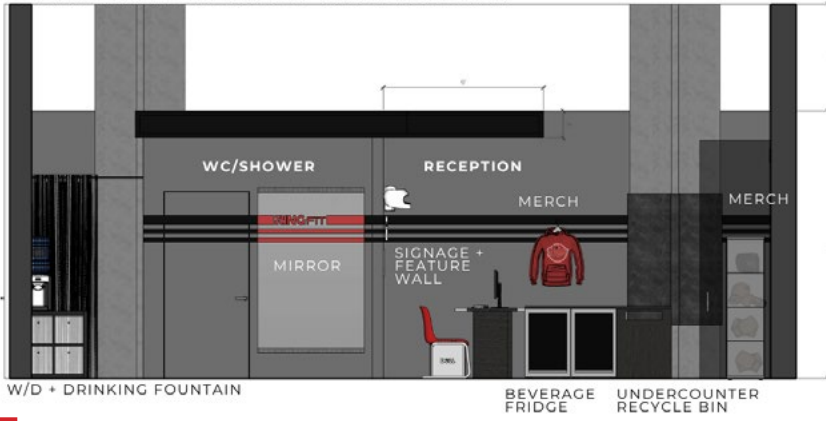

COLUMNS WRAPPED IN DISTRESSED MATTE BLACK LEATHER

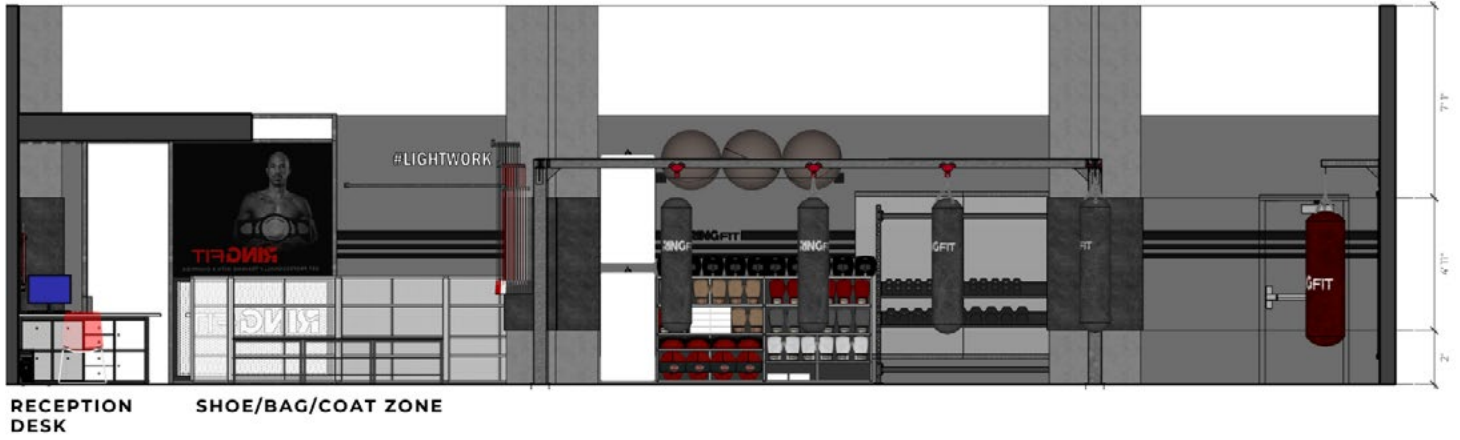



4

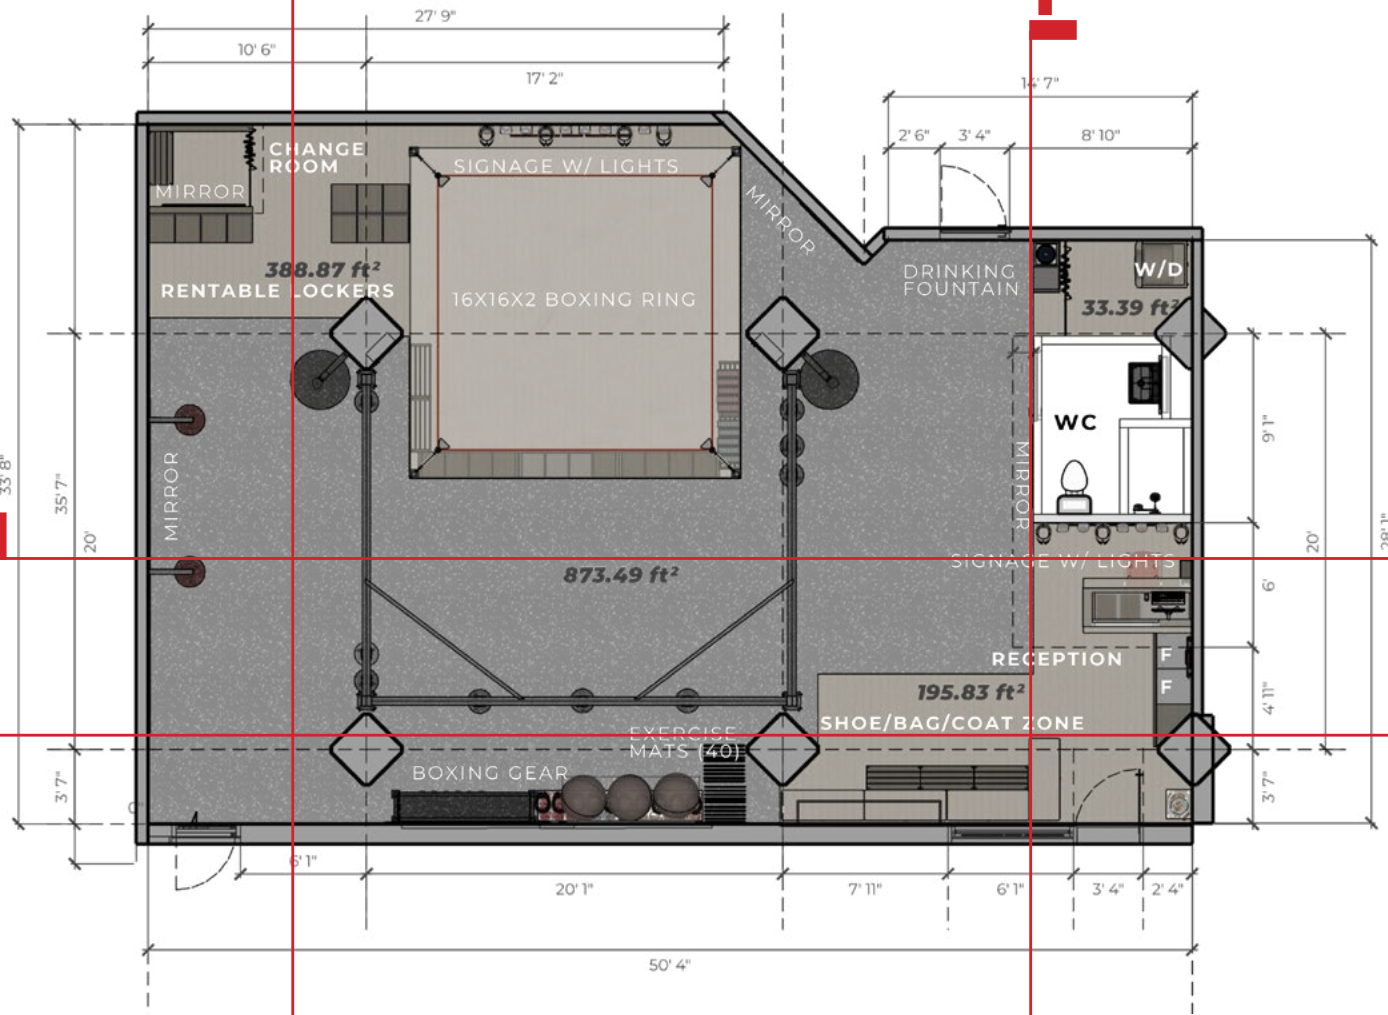


3

12

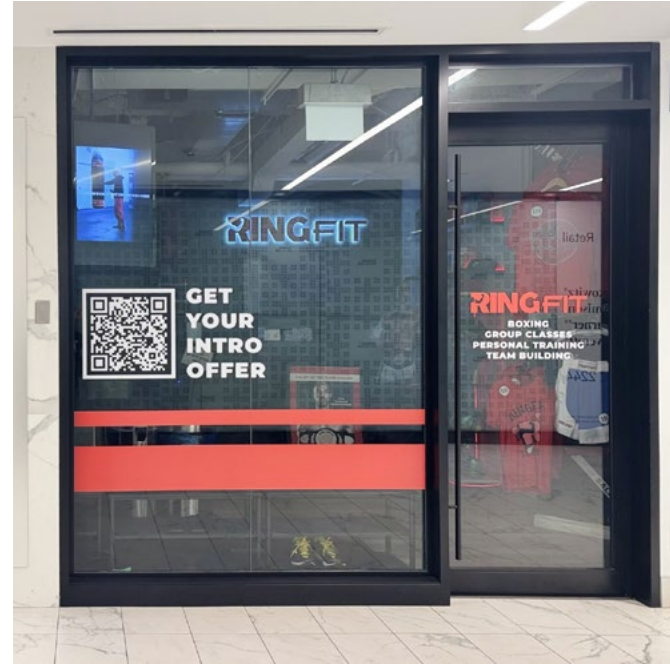

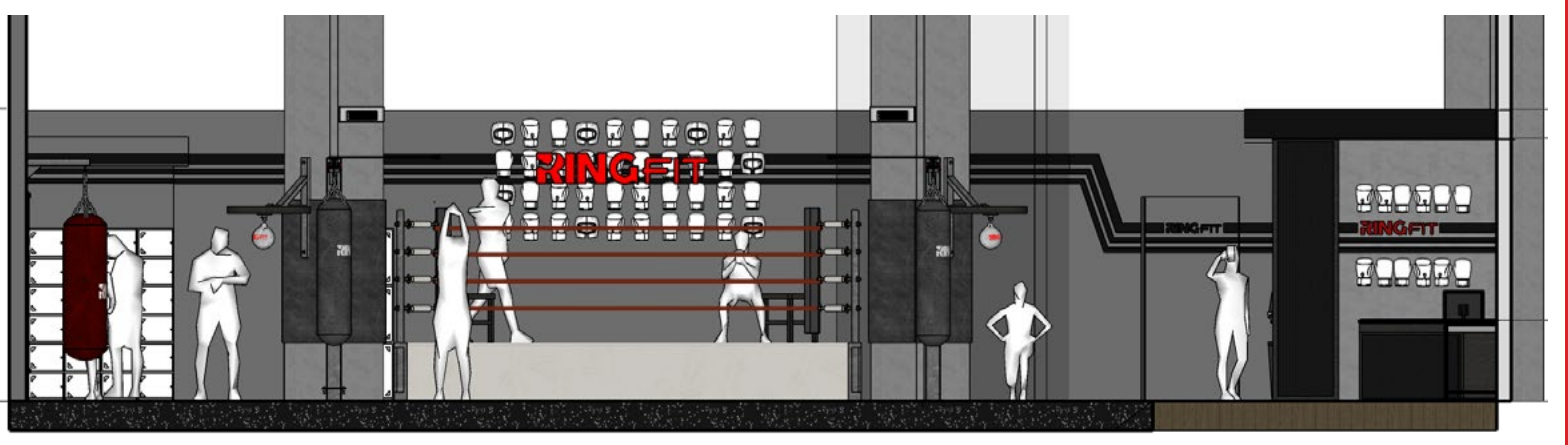

4

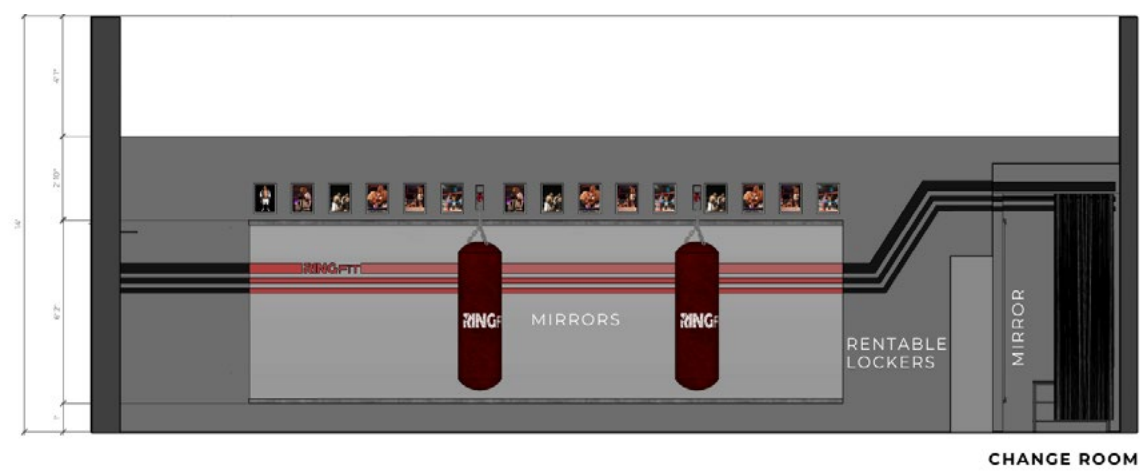

3







2021 **SMOQUE N' BONES**
BBQ RESTAURANT & WHISKEY BAR
SKETCHUP + LAYOUT

CLIENT
Confidential | 30 Baldwin St, Toronto, ON M5T 1L3


FROM CONCEPT TO BUILD

This project marks my first hospitality millwork package to be fabricated and built on site for a BBQ restaurant and whiskey bar. It was also my first solo millwork detailing effort, requiring careful coordination between design intent, material selection, and constructability to support a durable, high-traffic food and beverage environment.

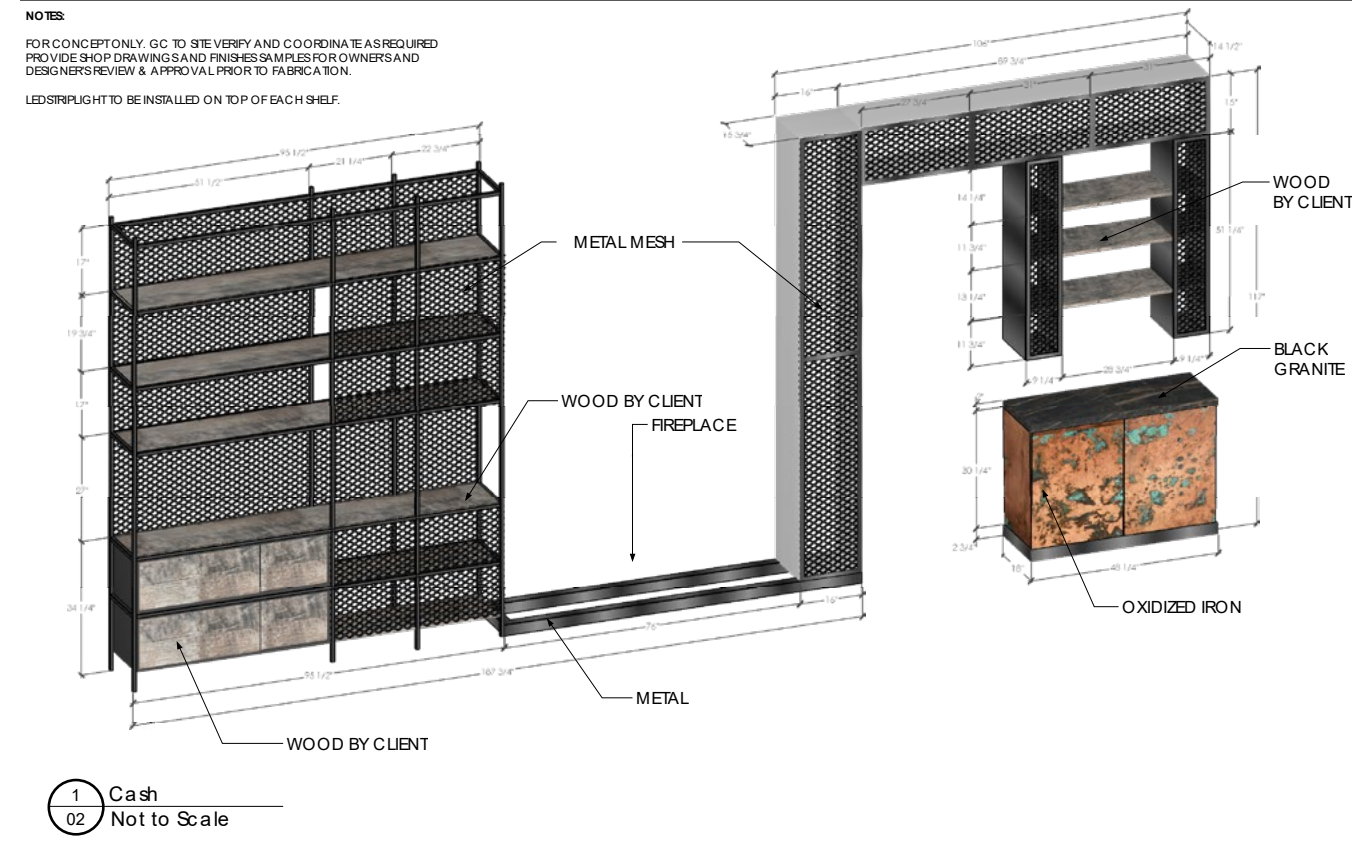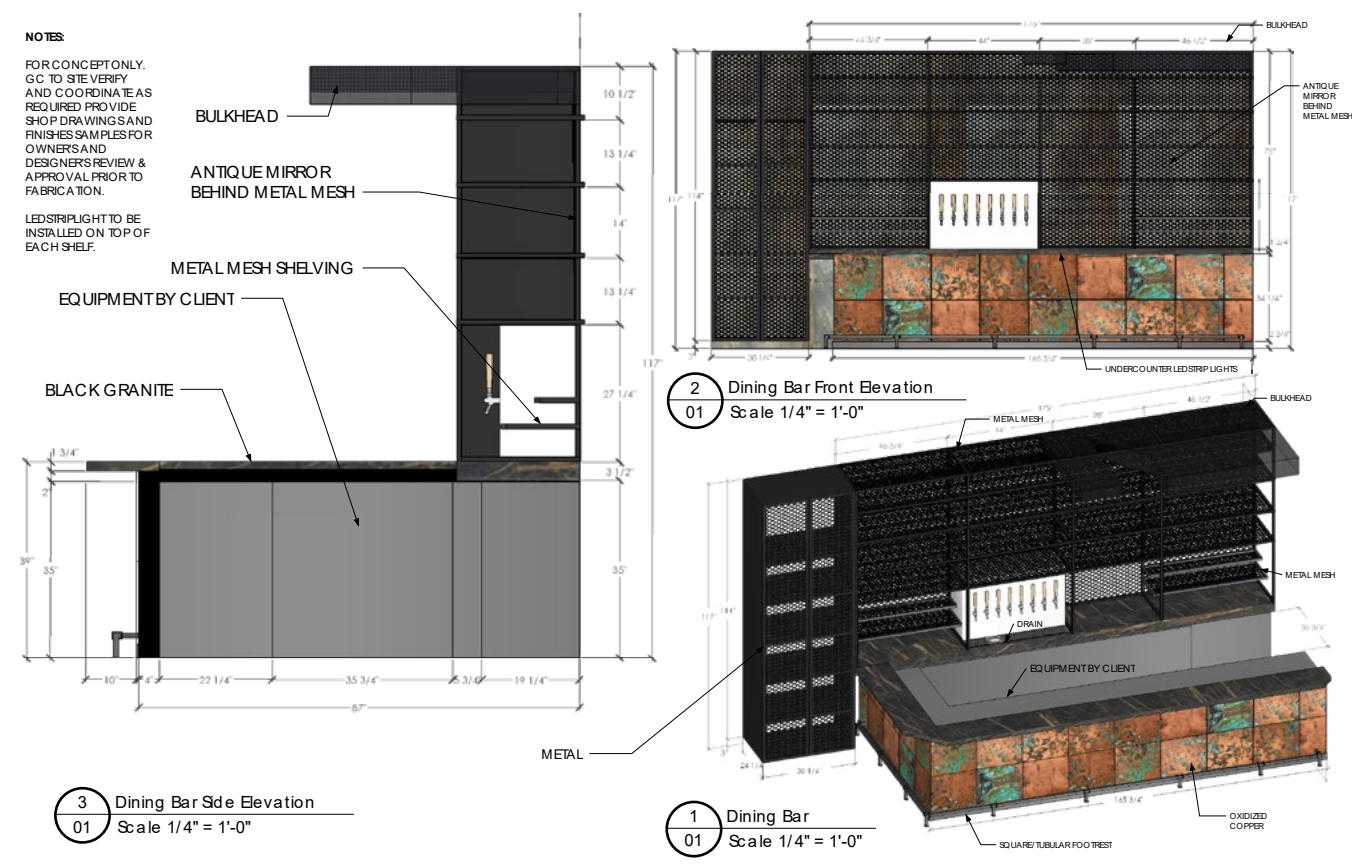



NOTES:
FOR CONCEPT ONLY. GC TO SITE VERIFY AND COORDINATE AS REQUIRED. PROVIDE SHOP DRAWINGS AND FINISHES SAMPLES FOR OWNERS AND DESIGNERS REVIEW & APPROVAL PRIOR TO FABRICATION.

LED STRIPLIGHT TO BE INSTALLED ON TOP OF EACH SHELF.

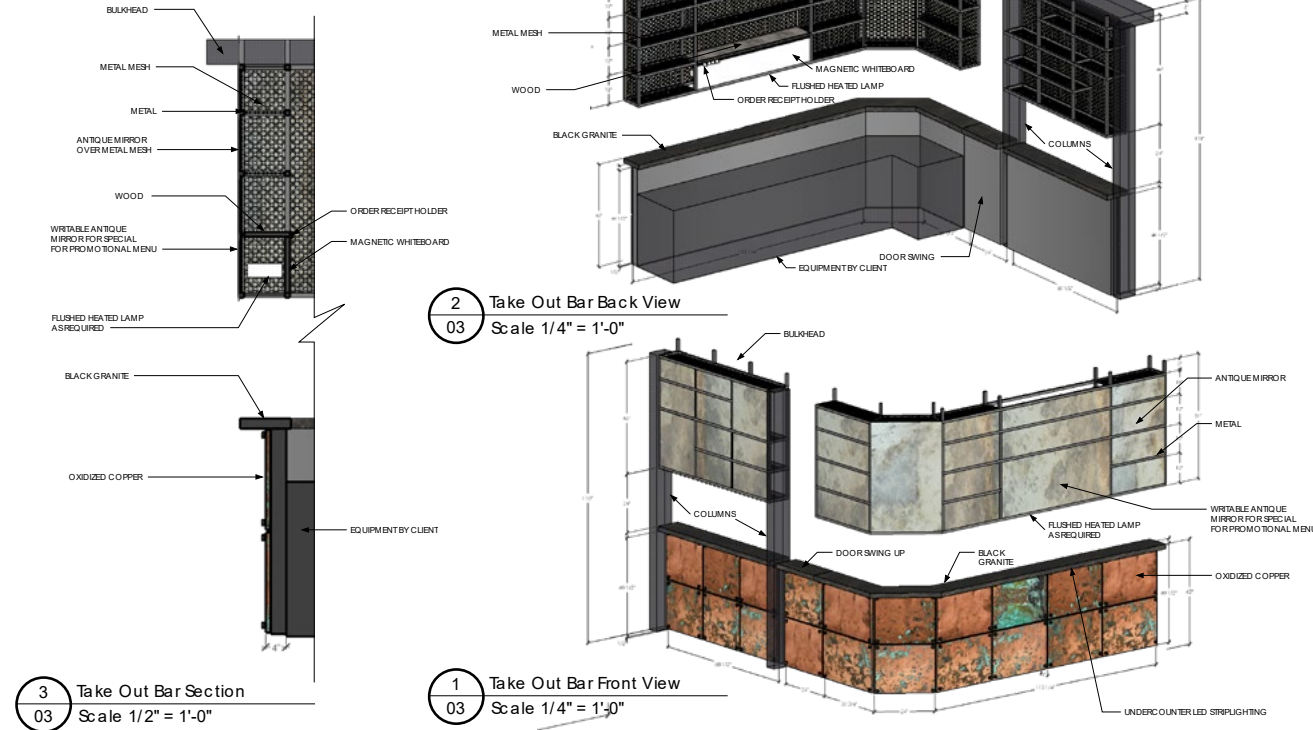

NOTES:
FOR CONCEPT ONLY. GC TO SITE VERIFY AND COORDINATE AS REQUIRED. PROVIDE SHOP DRAWINGS AND FINISHES SAMPLES FOR OWNERS AND DESIGNERS REVIEW & APPROVAL PRIOR TO FABRICATION.

LED STRIPLIGHT TO BE INSTALLED ON TOP OF EACH SHELF.

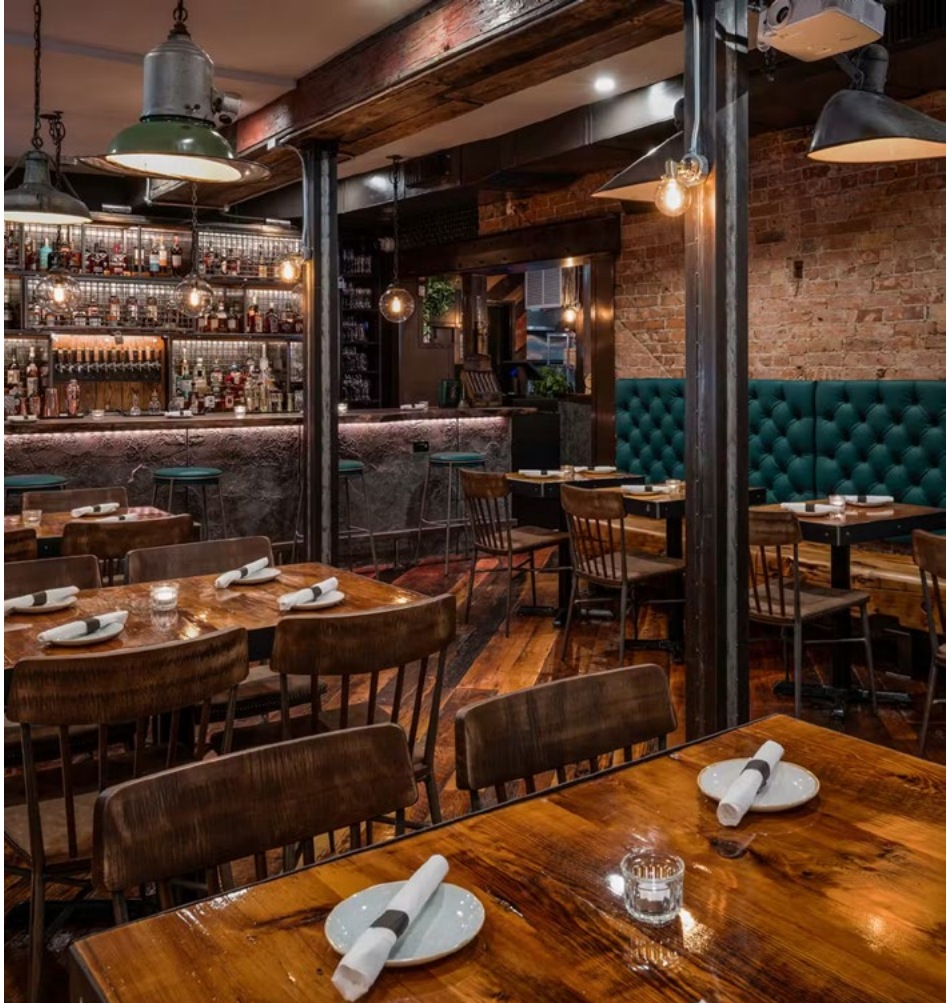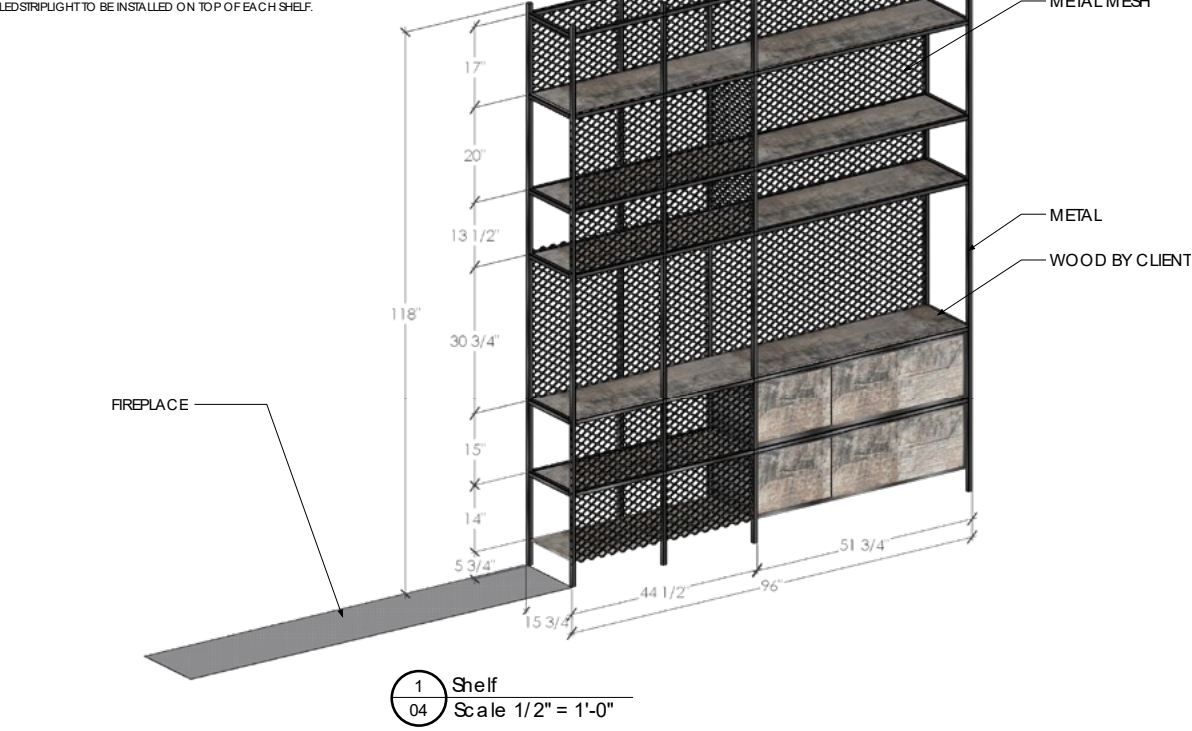



2022 LAKEVIEW

SALES CENTRE

SKETCHUP + LAYOUT

CLIENT

Confidential | 985 Hydro Rd. Mississauga, ON, L5E 0A8

This project involved the design development of a sales centre, translating a nature-inspired concept into a refined, buildable interior. The work focused on coordinating design intent across 3D modeling and technical drawings to support an evolving design process.

SCOPE OF WORK

- Revised the 3D model to reflect ongoing design changes
- Produced coordinated floor plans, elevations, and isometric views
- Developed detailed millwork drawings for design coordination and fabrication.



FROM CONCEPT TO BUILD

This project marked my first experience seeing millwork drawings I prepared fully fabricated and built on site. The completed project closely matched the original renders, highlighting the value of accurate detailing and clear communication from concept through construction.

CONCEPT

The design concept is inspired by the **BIRCH TREE**, drawing from its light tones, vertical rhythm, and subtle texture. These qualities informed material choices and millwork detailing, creating a space that feels calm, warm, and approachable while maintaining a clean, contemporary expression.



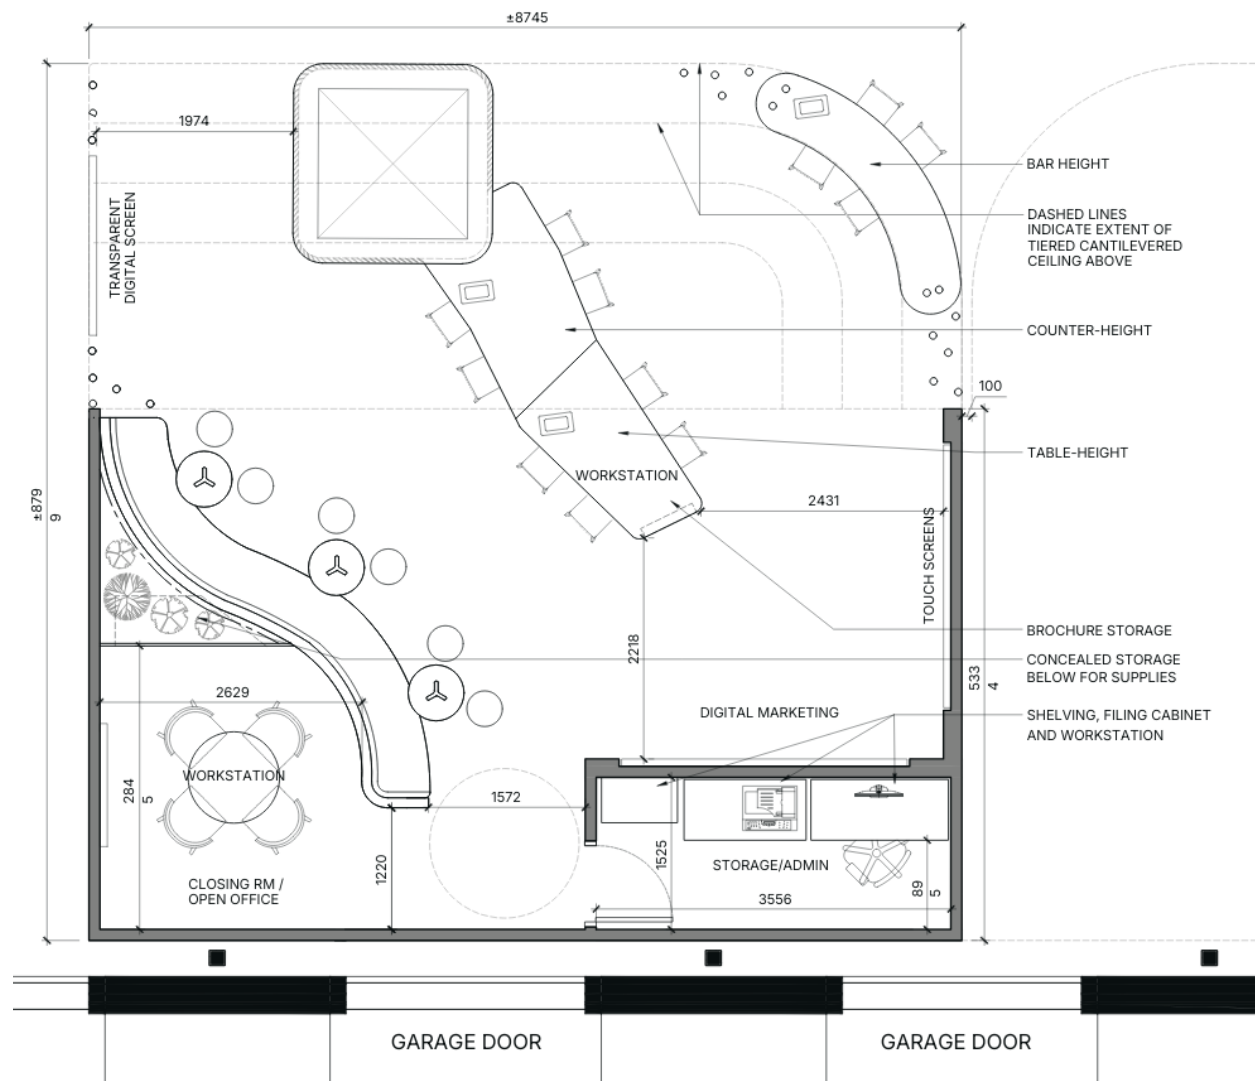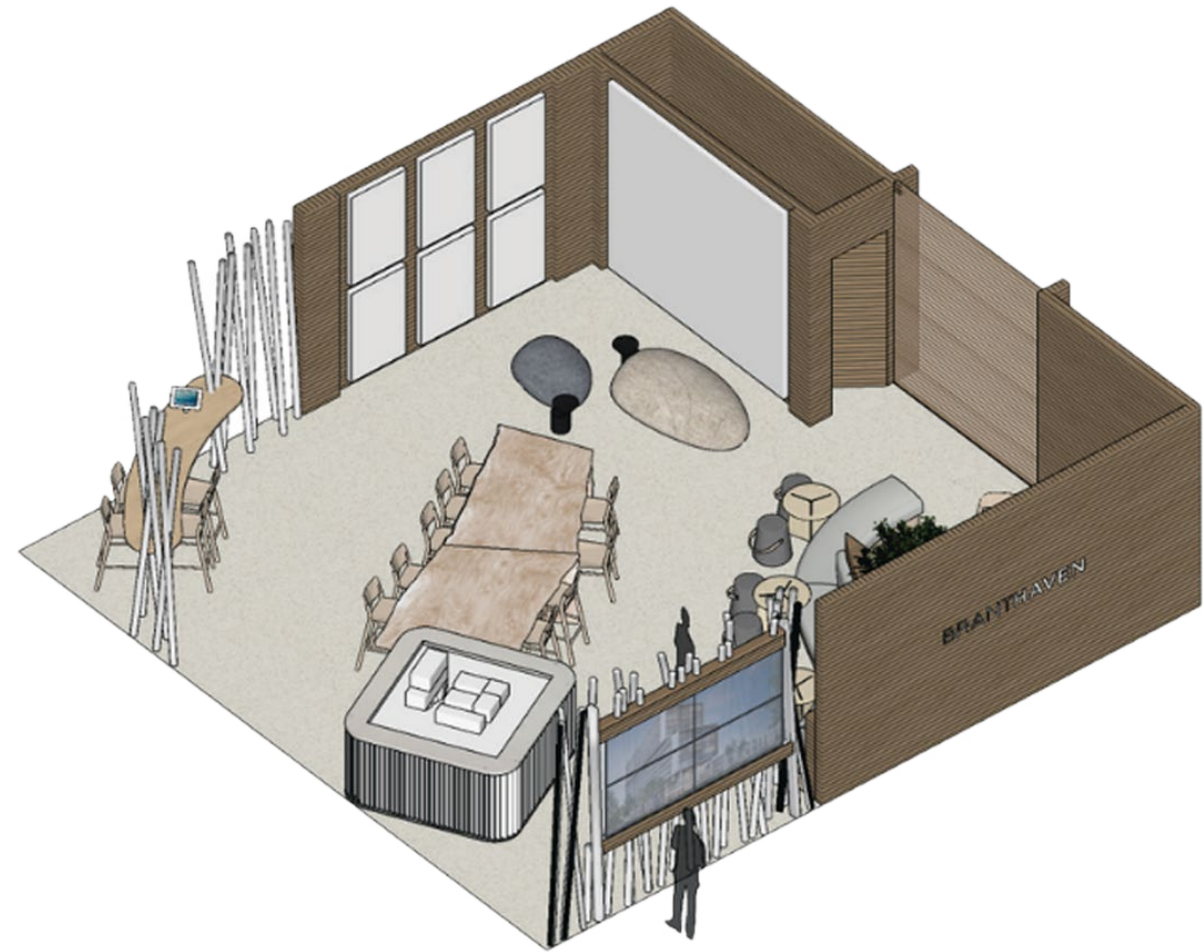



2021

ATTICA

RESTAURANT

REVIT + ENSCAPE

Recipient Of Pizzale Design Award 2022

CLIENT
Ben Shewry | Melbourne, Australia

Ben Shewry is a chef known for using locally sourced and native Australian ingredients—many unfamiliar even to Australians. His cooking is grounded in nature, culture, and a deep respect for the land.

The design reflects this philosophy through natural materials, earthy textures, and simple, honest forms—creating a space that feels rooted, authentic, and quietly innovative.


MENU | “First Nations’ stories and foods are celebrated, not claimed” (Valent, 2019)




Besha Rodell. (2019, October 23). Yes, Attica Is Worth It: What Makes Ben Shewry’s Restaurant Special. Retrieved October 14, 2021, from Eater website: <https://www.eater.com/2019/10/23/20918617/attica-melbourne-review-ben-shewry-tasting-menu>

CONCEPT
ARCHIPELAGO takes inspiration from a group of islands—each unique, yet connected by the same waters. Like landforms scattered across the sea, the design brings together distinct elements that celebrate diversity while creating a unified whole.

Grounded in the contrast and harmony of **EARTH** and **WATER**, the concept reflects **INCLUSIVITY** and Melbourne’s multicultural identity. Through varied forms, textures, and materials, Archipelago becomes a space where individuality is embraced and **UNITY** is felt.

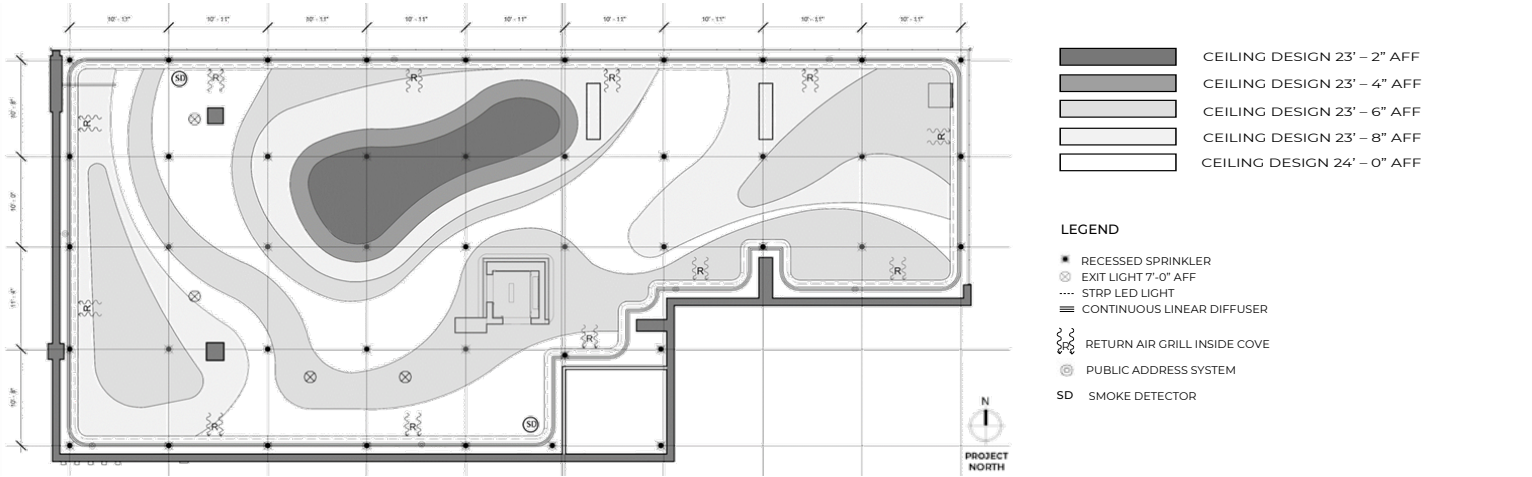


PART I

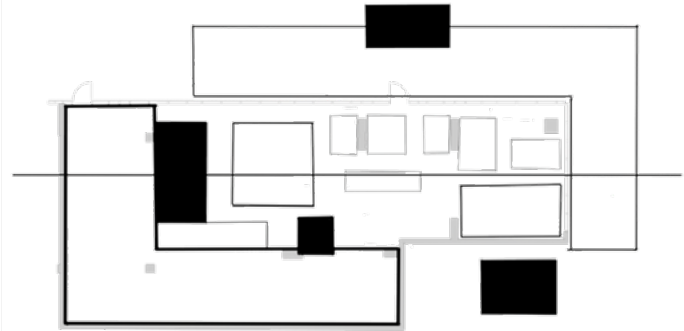

ORIENTATION
Both the site plan and the building are aligned toward the water, emphasizing a strong visual and spatial connection to the waterfront.

CLUSTER ORGANIZATION
The project’s layout reflects the linear patterns of surrounding traffic routes and the fragmented yet unified nature of an archipelago, forming a cluster of interconnected structures.

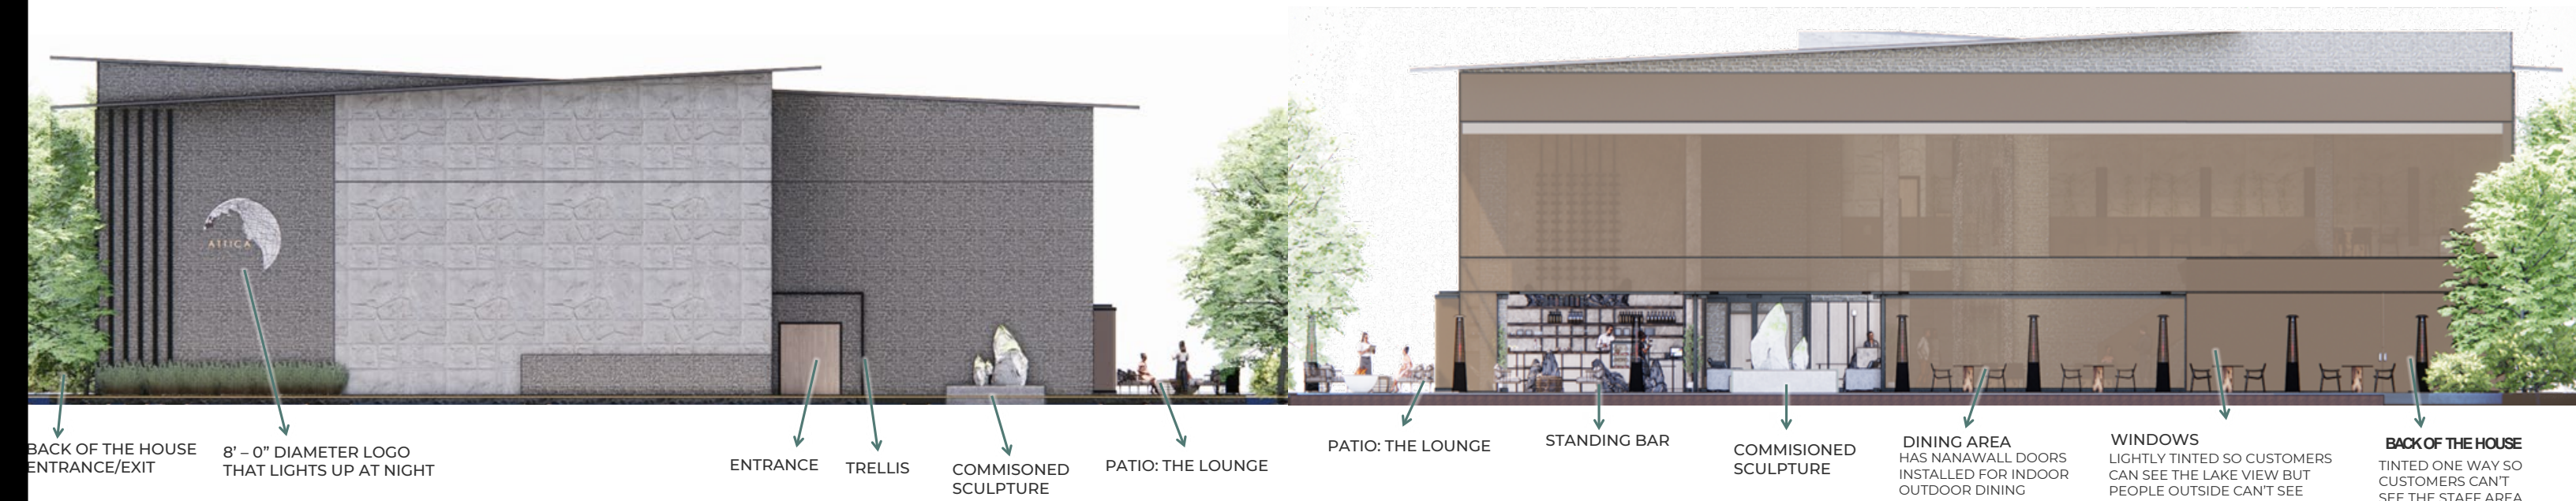

THE LOUNGE

A welcoming space where guests can enjoy drinks, scenic views, and a cozy water-vapour fireplace. Furnished with textiles by women-led Melbourne studios in partnership with Indigenous artists.



VESTIBULE

Continuous trellis bridges exterior and interior. Sliding doors ensure seamless access.



GLASS ELEVATOR



Projection-mapped glass elevator transforms into an immersive, sustainable celebration display.

RECEPTION & COAT CHECK

Material palette of rough stone, marble, and wood creates a balanced visual harmony.

RECEPTION DESK IDEATION PROCESS




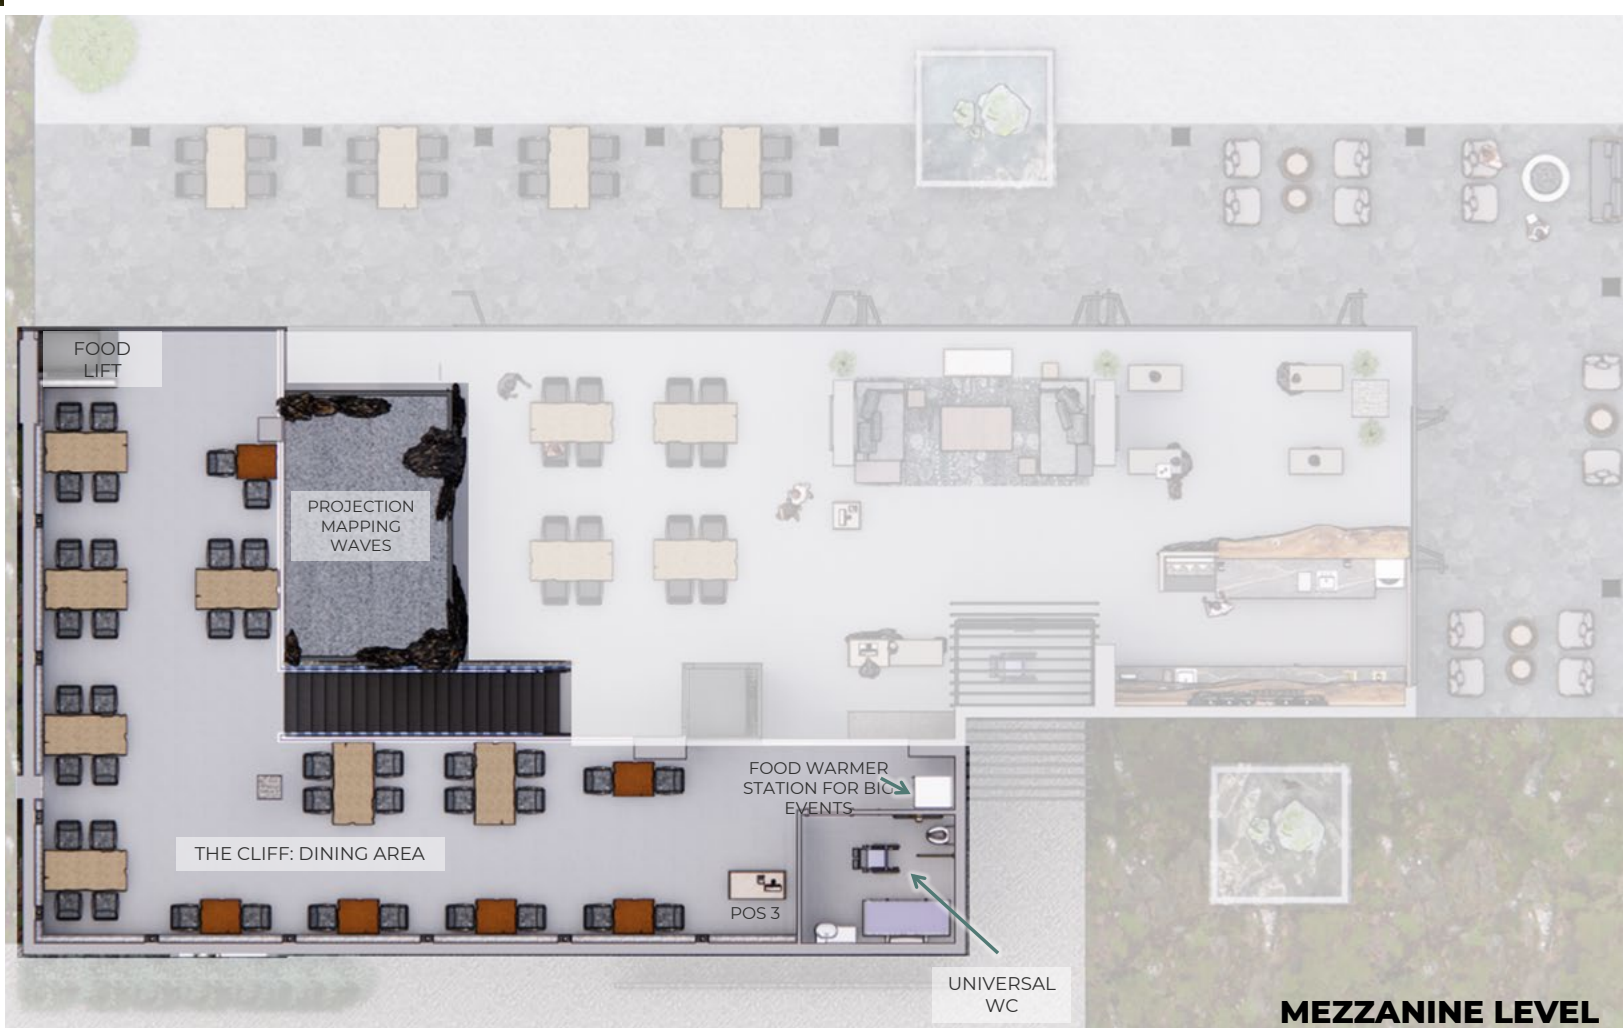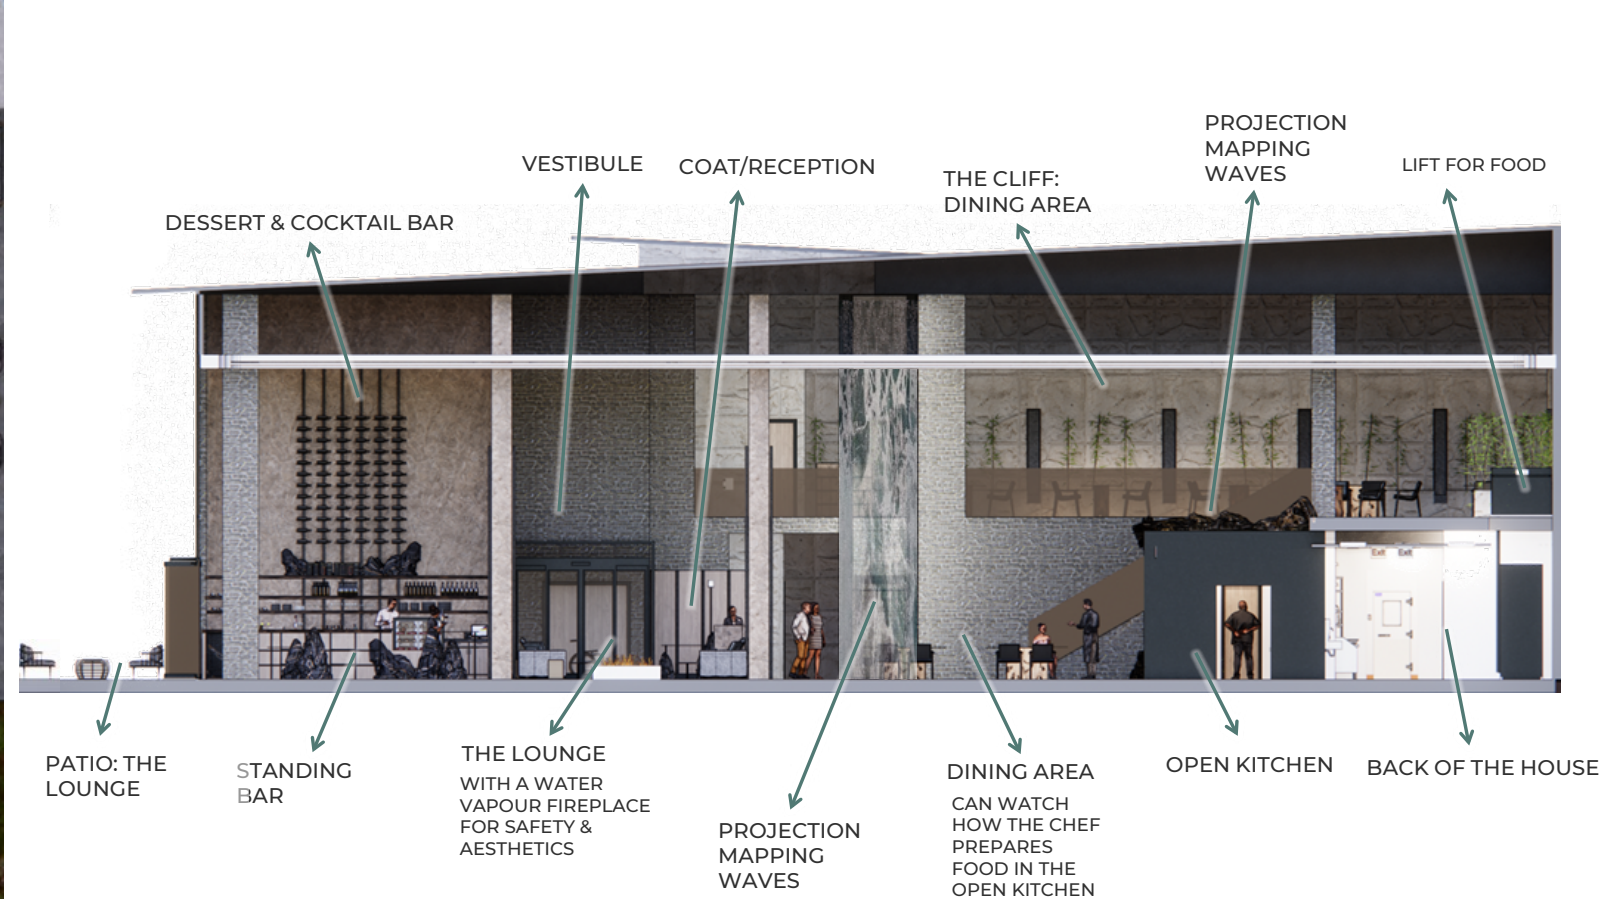



DESSERT & COCKTAIL BAR

A sleek walk-in space offering desserts, cocktails, and locally sourced wine and beer. An undercounter espresso setup supports Australia's strong coffee culture while maintaining a clean, minimalist look.

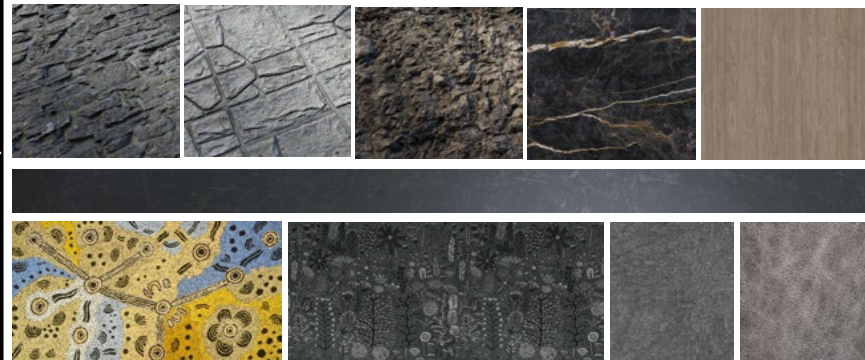

MATERIALS – WALL, FLOOR & TEXTILE

A contrast of rough rock finishes reflecting the raw hardness of earth, balanced with soft textiles and warm wood to create a grounded yet inviting atmosphere.



DINING AREA

A reservation-only dining space offering guests a direct view of the chef crafting food as art. A dedicated host station includes a POS system and hidden storage for glassware and utensils. Operable NanaWalls provide a flexible indoor-outdoor experience—ideal for post-pandemic adaptability. Underlit stair nosings ensure safe circulation, while candlelit tables enhance warmth and ambient lighting.



KITCHEN STUDIO

A functional and culturally enriched space featuring stainless steel finishes that meet commercial kitchen hygiene standards. A commissioned mosaic tile wall, based on “Minma Kutjara” by Indigenous artist Maureen Baker, adds narrative depth—depicting two ancestral women transforming landscapes through their journey. Tiles were selected for their durability and ease of sanitation.



Equipment layout is modeled after a real closed fine-dining kitchen that has served multiple cuisines, including French, American, and contemporary Toronto fusion. Appliances include a range, griller, cheese melter, food warmer, French top, oven, refrigerator, freezer, and ceiling-mounted ventilation systems.




THE CLIFF – PRIVATE DINING

A reservation-only space designed for intimate or large private events. A discreet food lift in the corner streamlines service, allowing a single server with a cart to manage entire table settings—reducing labor costs and minimizing the risk of stair-related accidents.

The ceiling features an organic form inspired by earth and water, with integrated cove lighting and concealed air diffusers within the bulkhead. Wave projection mapping above the kitchen continues the immersive visual language from the elevator experience. Interior finishes are matched to the exterior for a seamless indoor-outdoor connection.

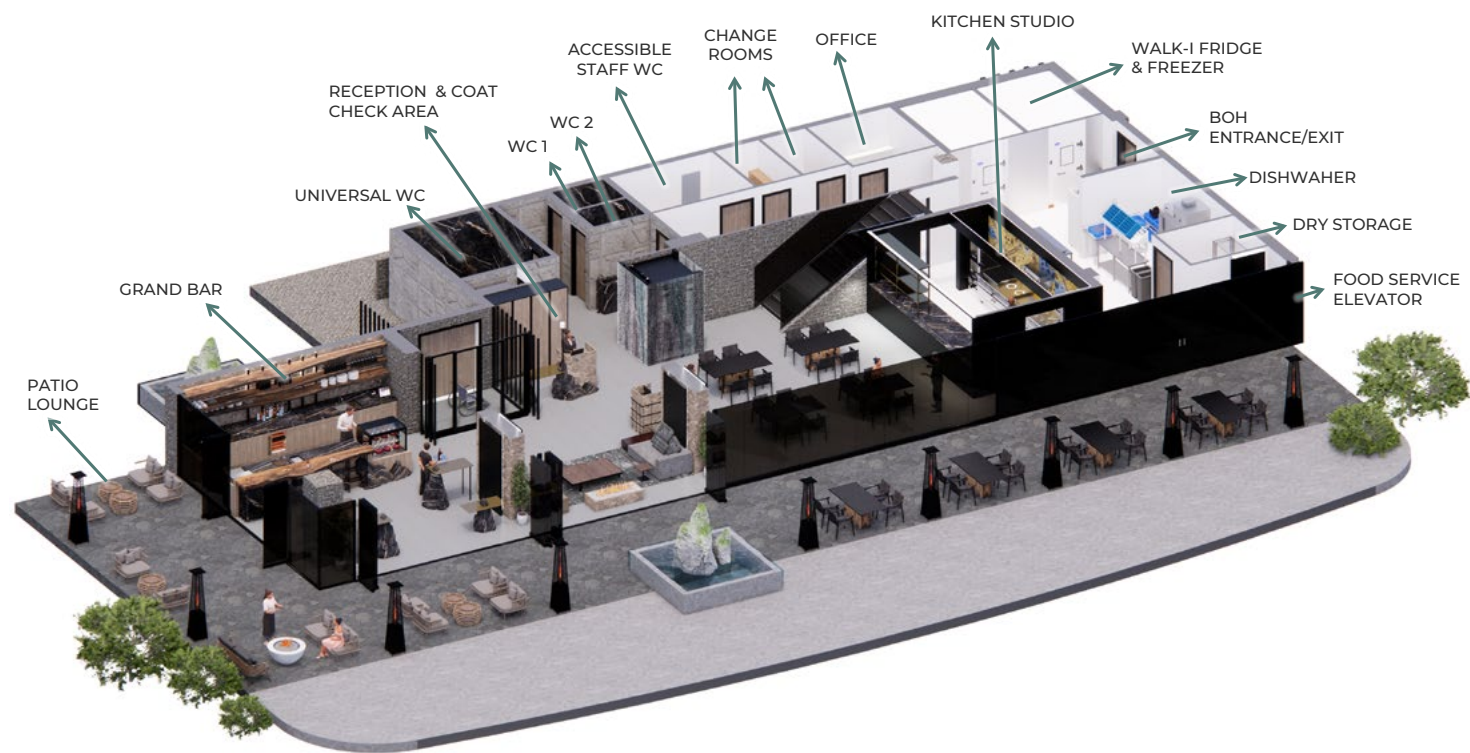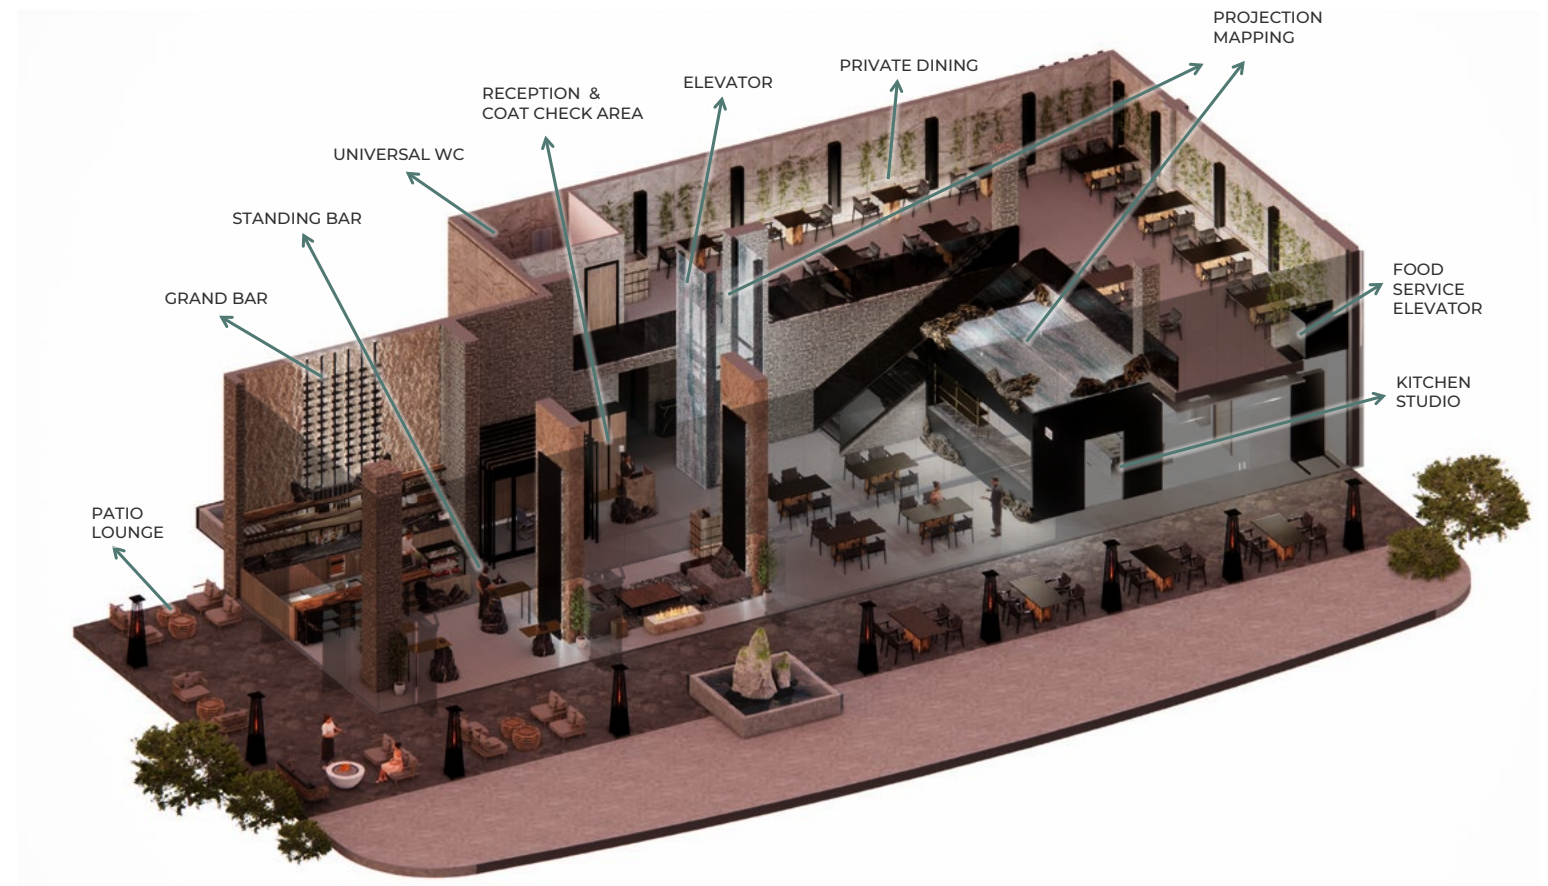

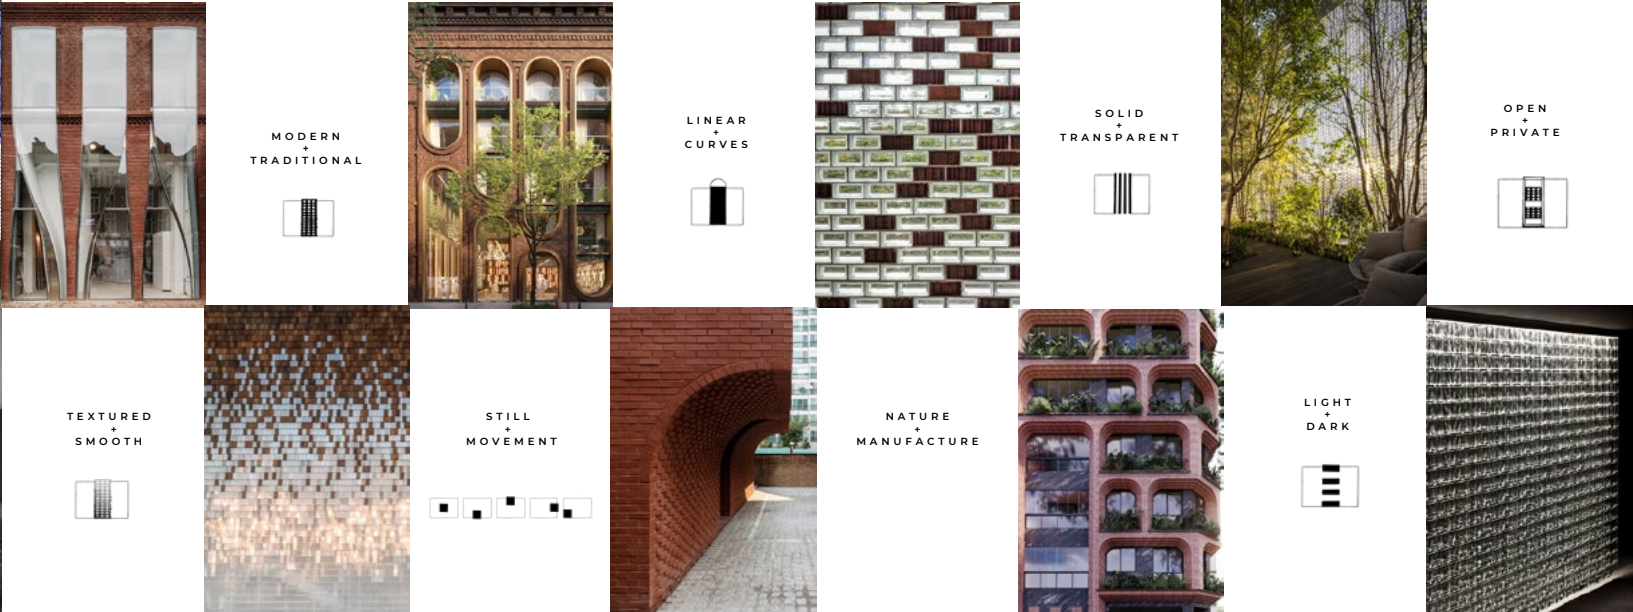

CONCEPT + DESIGN PROCESS



CON • TRAST
Noun /'kän, trast/
the state of being strikingly different from something else in juxtaposition or close association.

2024 **OASIS**
WELLNESS HUB
SENIOR LIVING
REVIT + LUMION

The thesis project revolves around the development of a senior community center, drawing inspiration from personal experiences, notably the journey of the designer's mother. The study recognizes the paramount importance of Aging in the Right Place (AIRP) and is determined to create an enriching space tailored specifically for Naturally Occurring Retirement Communities (NORCs).

CLIENT
Senior Community Centre | 21 Ossngton Avenue

Through strategic integration of cutting-edge technology, the project design aims to simplify administrative tasks, enabling staff to focus on fostering meaningful human connections within the NORC setting. This social building stands as a to addressing societal needs through innovative design solutions, with a strong emphasis on enhancing the quality of life for seniors.






LEGEND:

- Major adjacency
- Minor Adjacency
- Open
- High Acoustic
- Plumbing




FIRST FLOOR

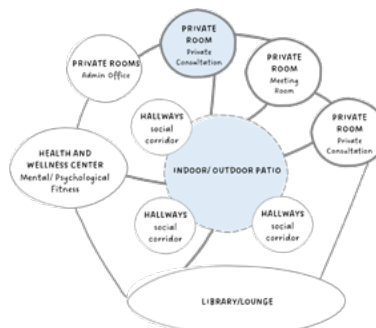


SECOND FLOOR


BUBBLE DIAGRAM

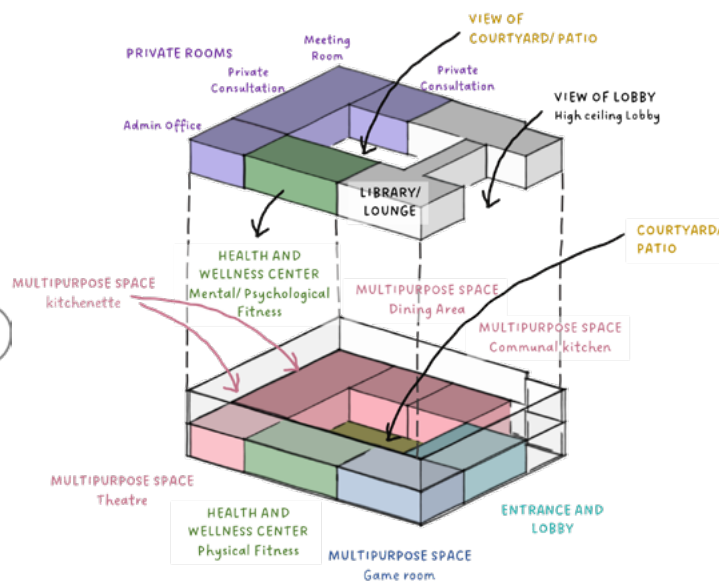


BUBBLE DIAGRAM ON EXPLODED ISOMETRIC PARTI

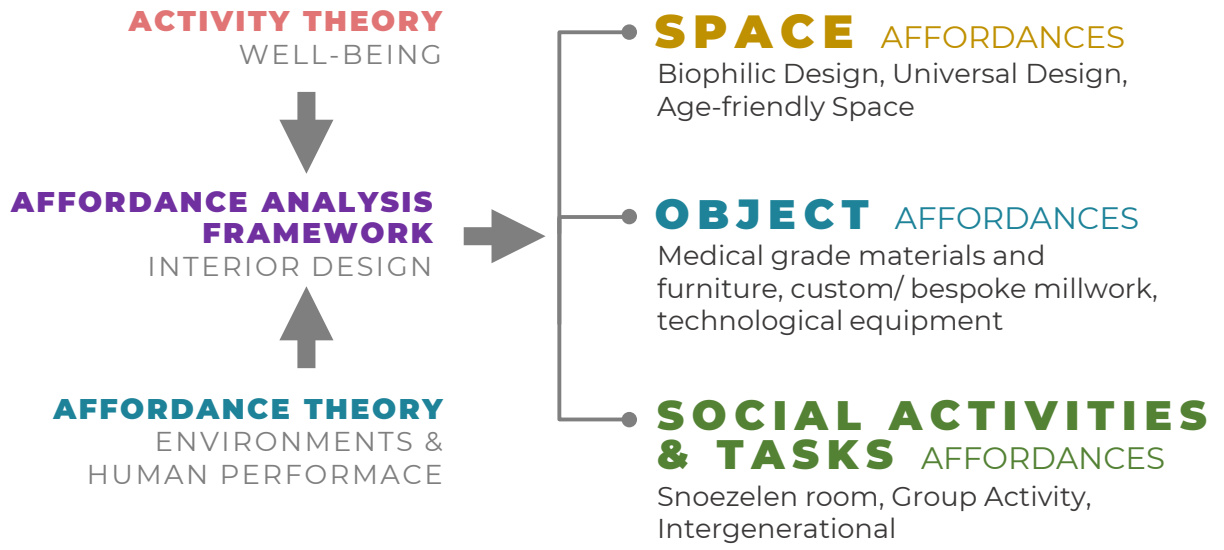


Affordance Analysis Framework on Senior Community Centre
CONCEPTUAL FRAMEWORK

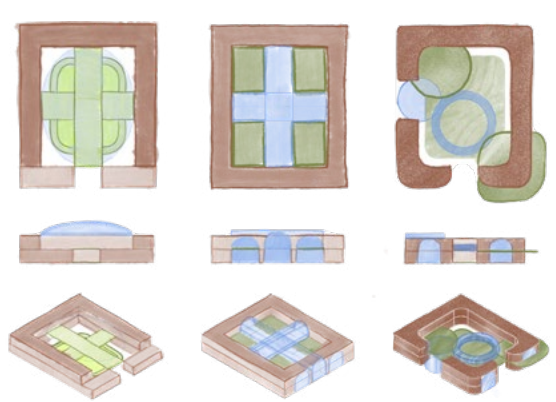


PARTI

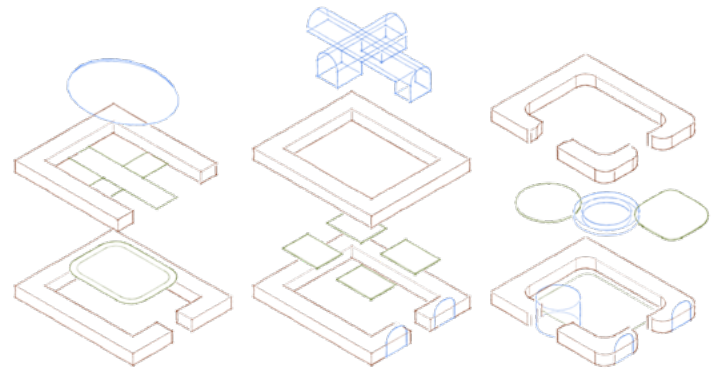


EXPLODED ISOMETRIC PARTI

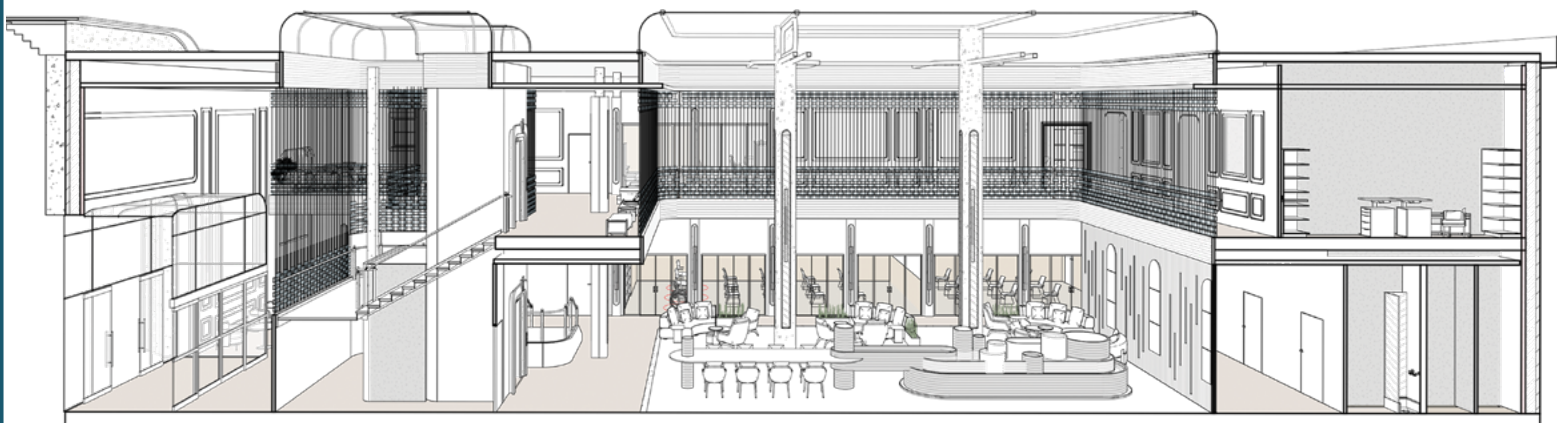

INDOOR COURTYARD

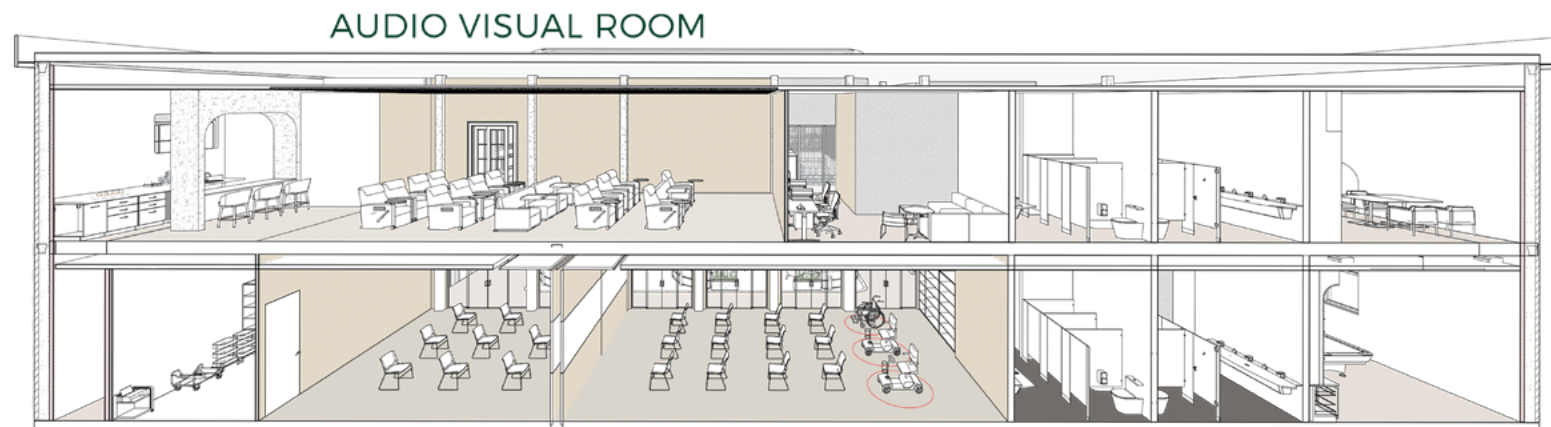

AUDIO VISUAL ROOM

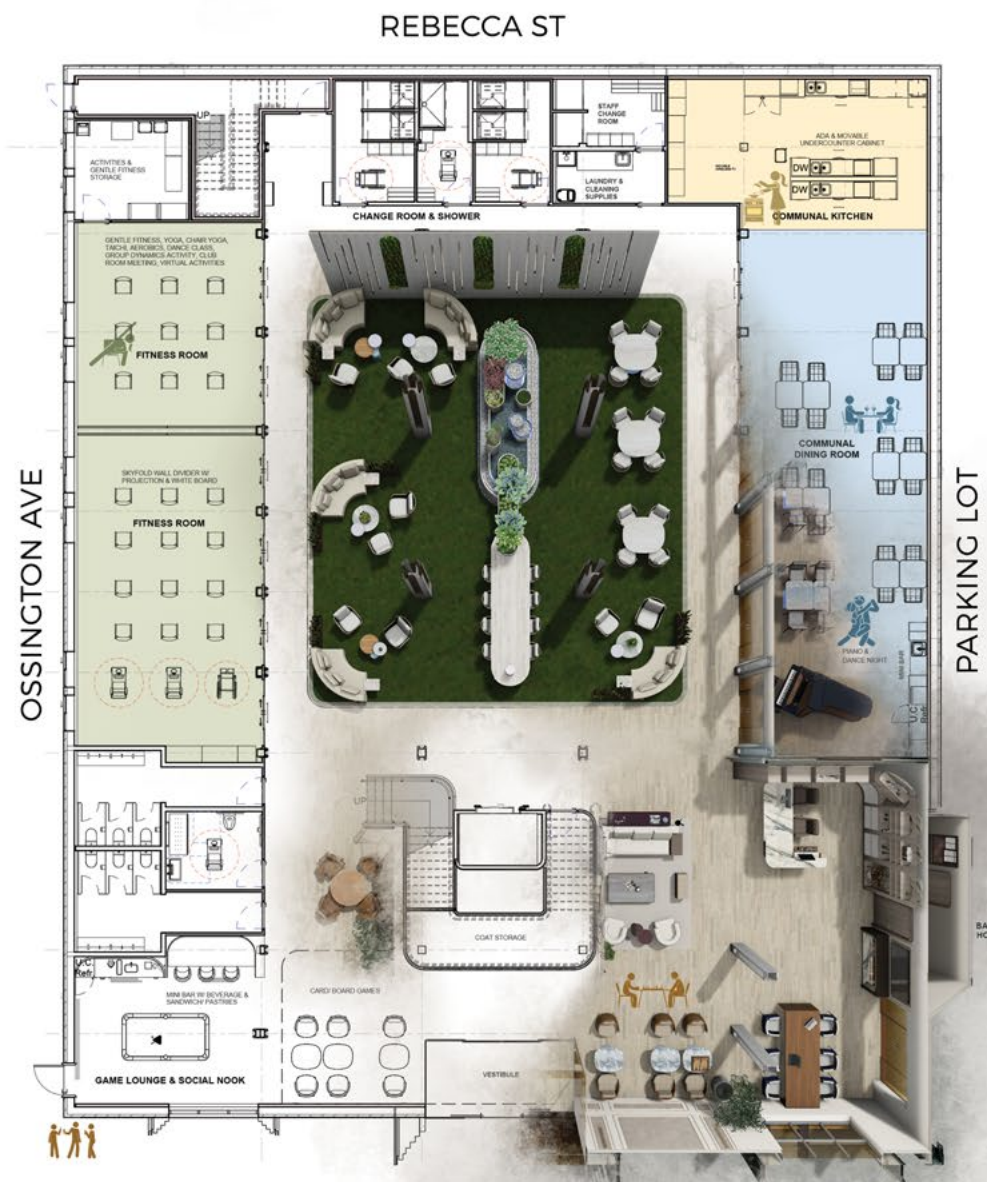


OSSINGTON AVE

REBECCA ST

PARKING LOT



FIRST FLOOR

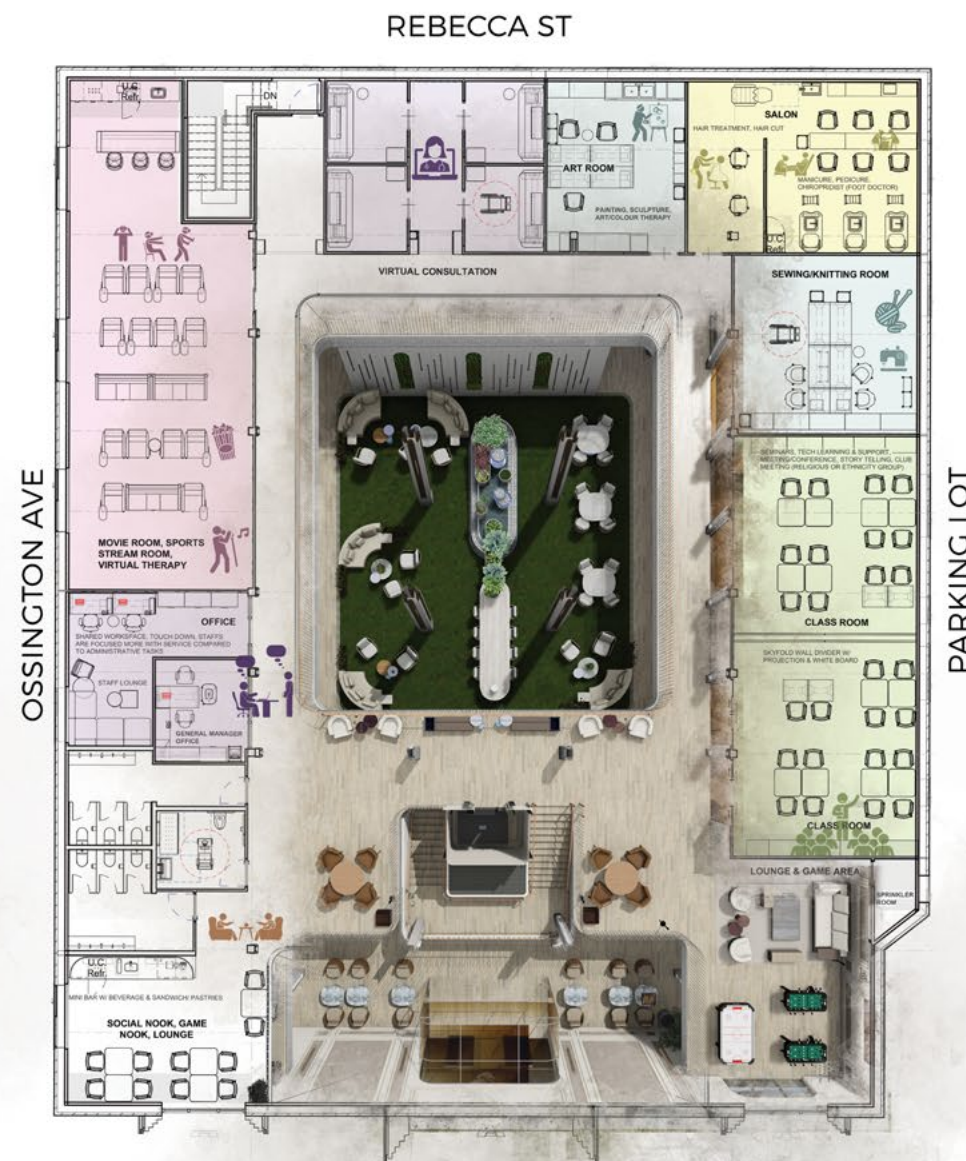

OSSINGTON AVE


REBECCA ST













PARKING LOT







SECOND FLOOR



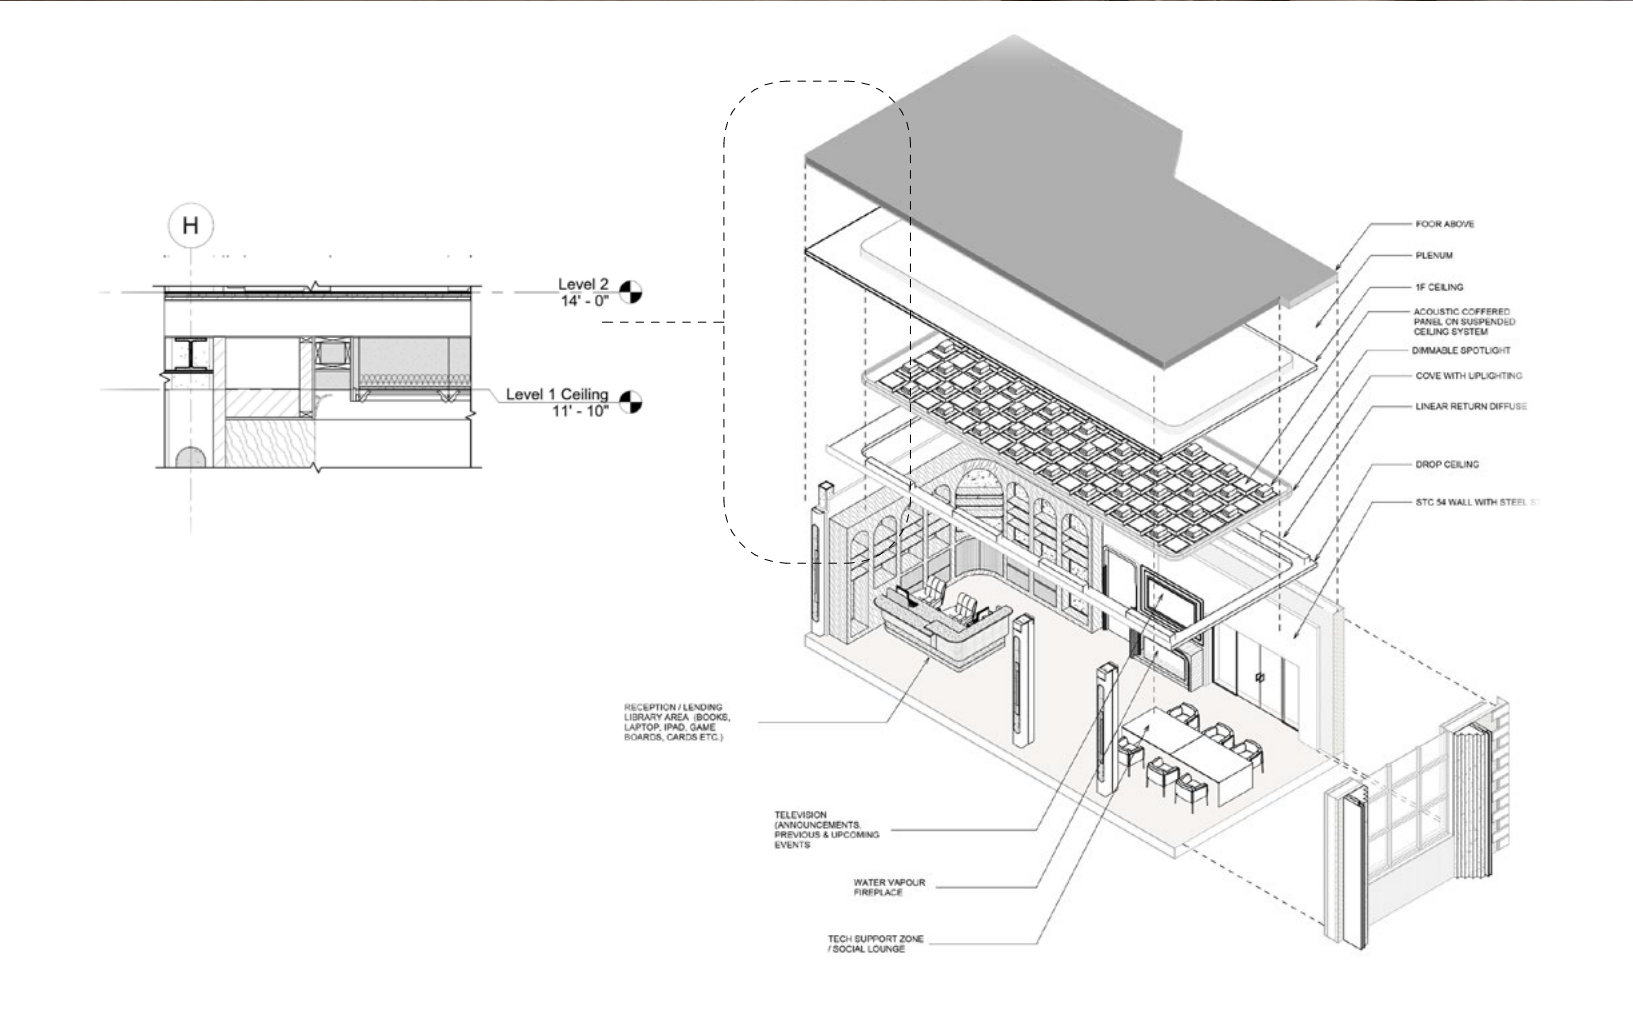

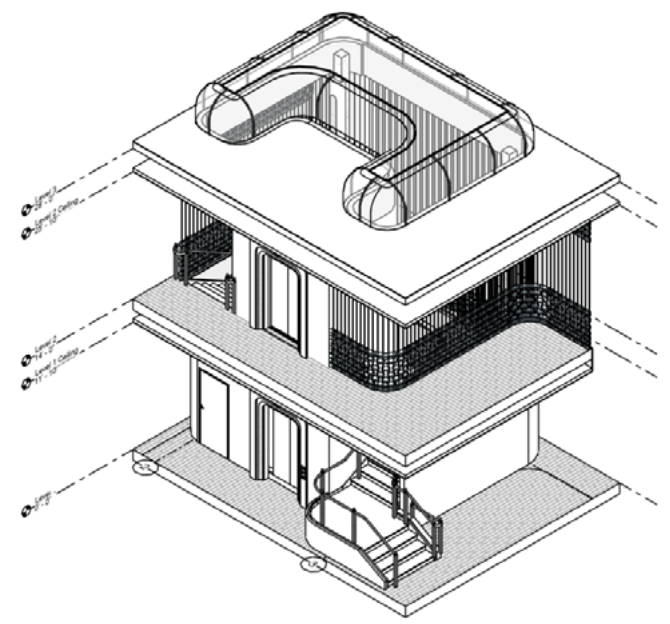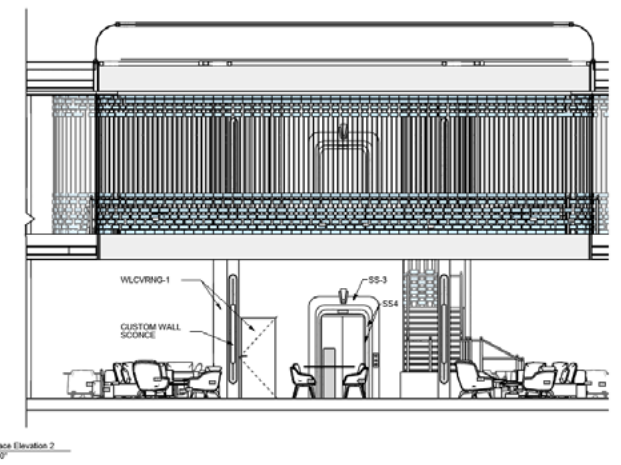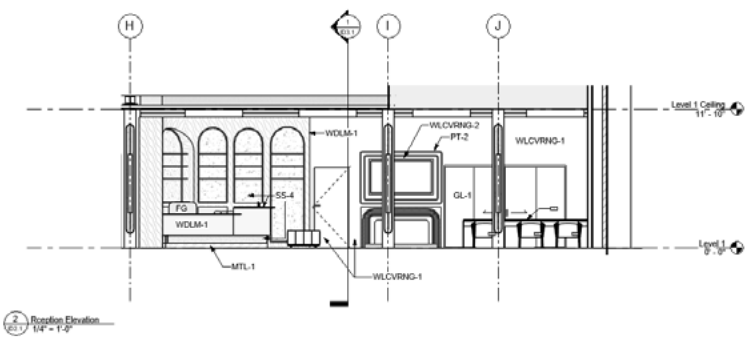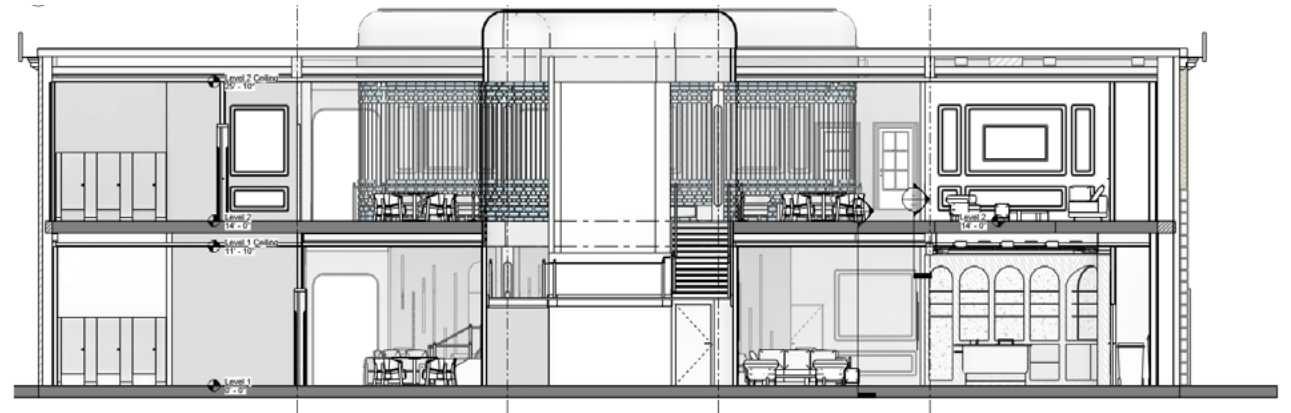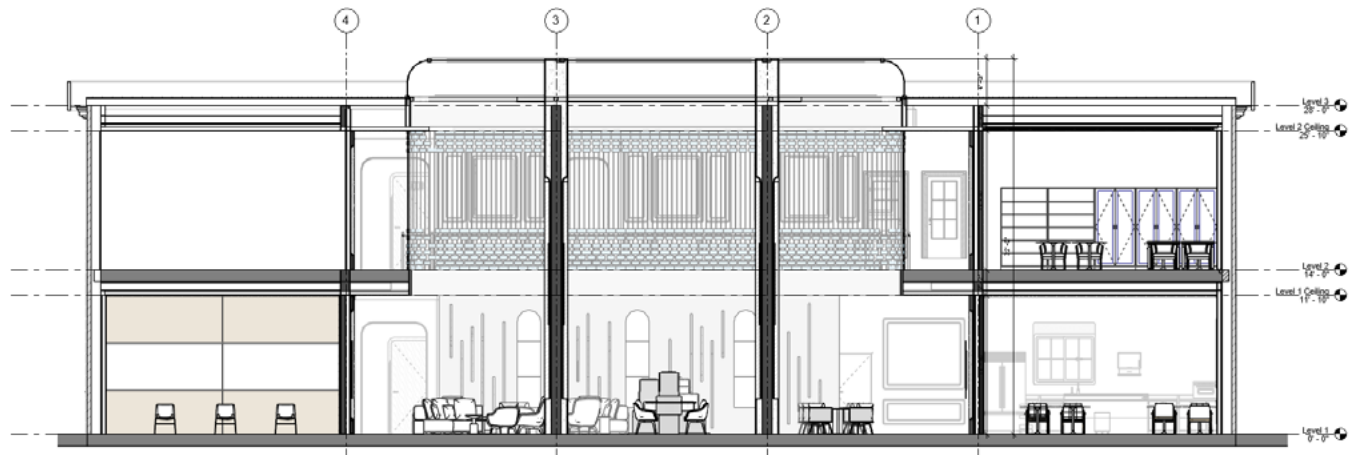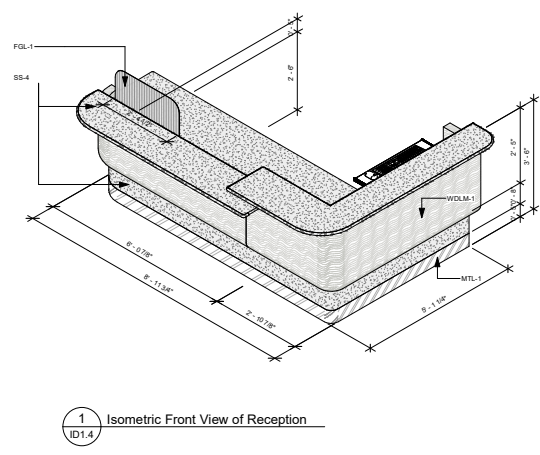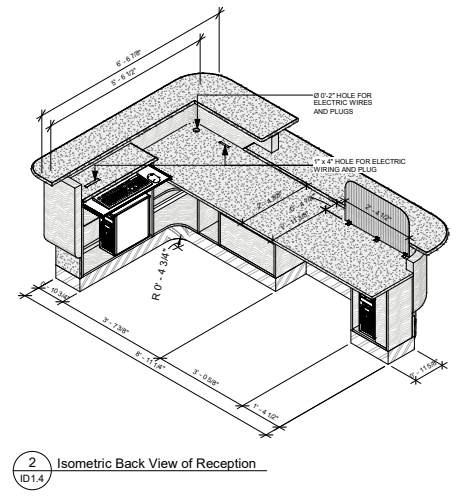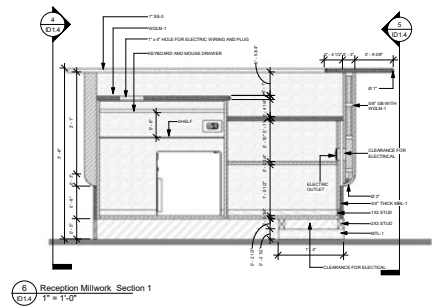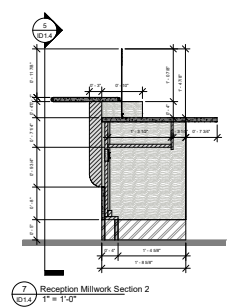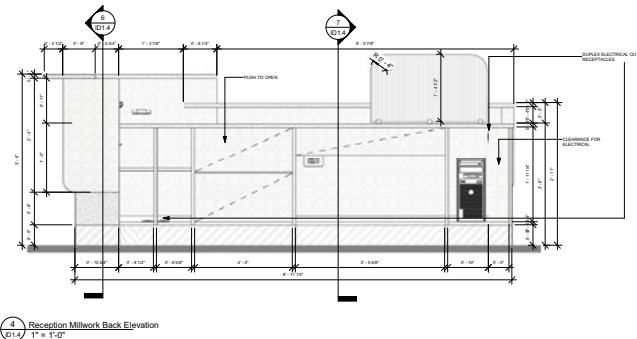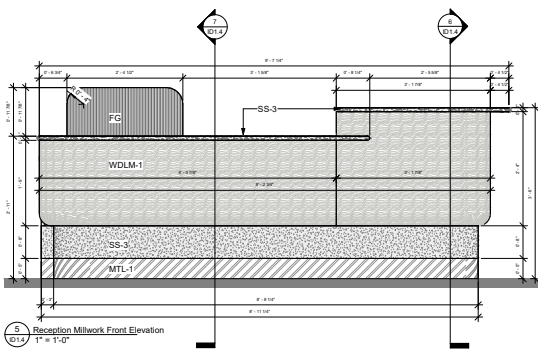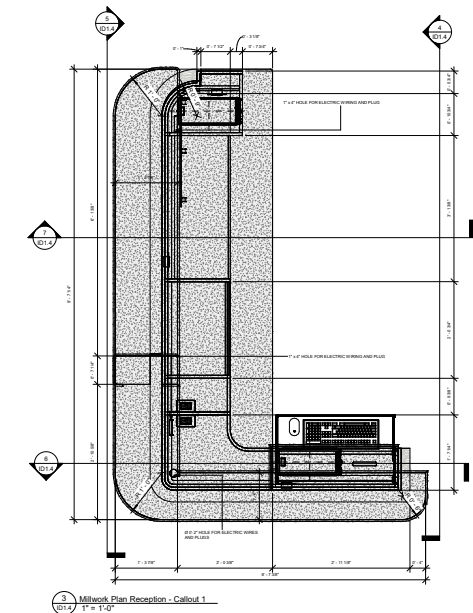

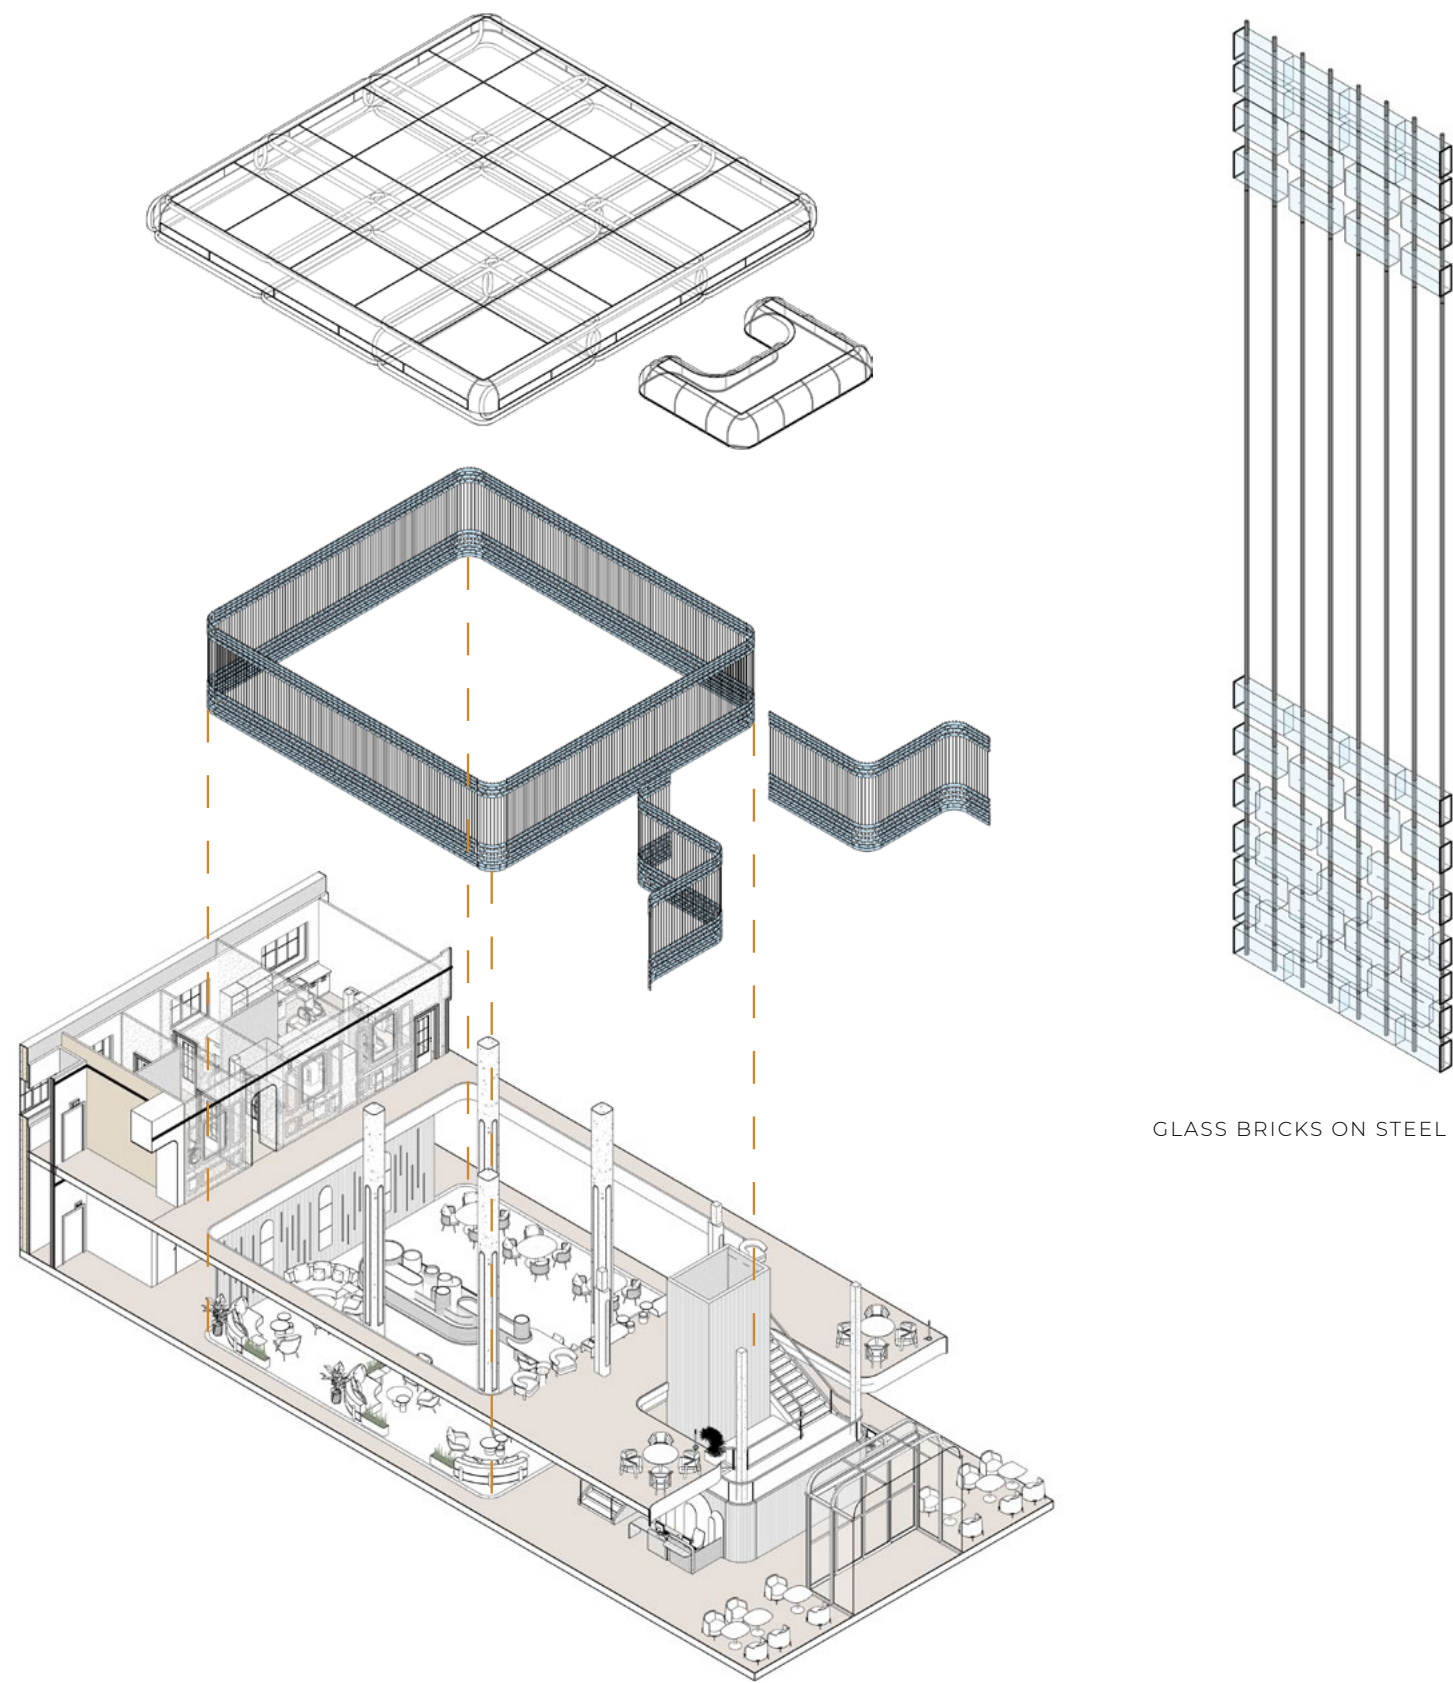

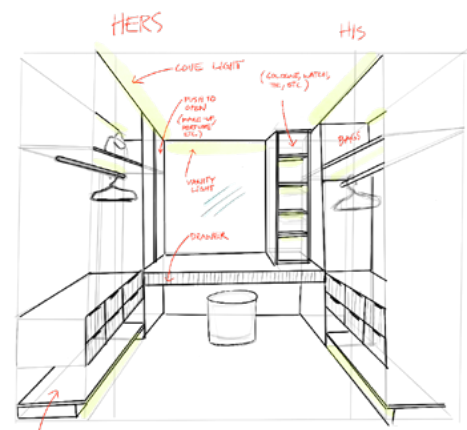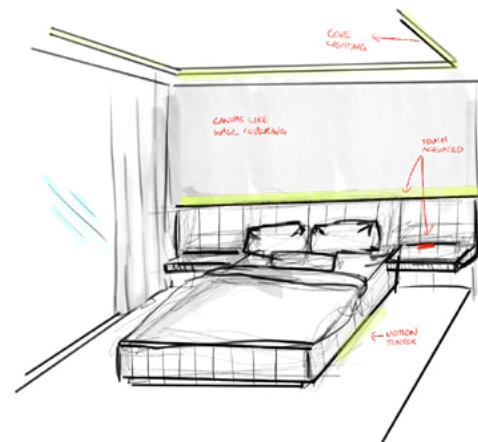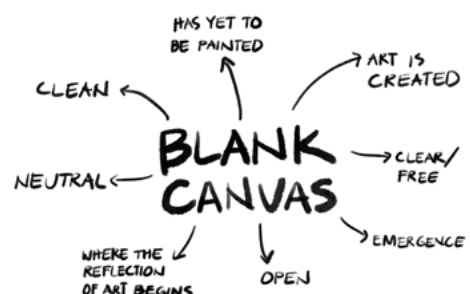

2020 LOFT

RESIDENTIAL

REVIT + ENSCAPE



CLIENT

The client is a couple where one works from home and sells Indigenous art. They want to use their apartment as an art gallery for their entire collection, so it's important that the art pieces are showcased and highlighted in the space. In addition, they also plan to sell the place in the future, so the palette should be able to match most people's tastes.

CONCEPT




BLANK CANVAS captures the spirit of creation—free, expressive, and emotionally charged. The design uses a neutral, timeless palette that lets the artwork shine while appealing to future buyers. Like an untouched canvas, the space invites imagination, allowing the art to speak and the home to breathe.



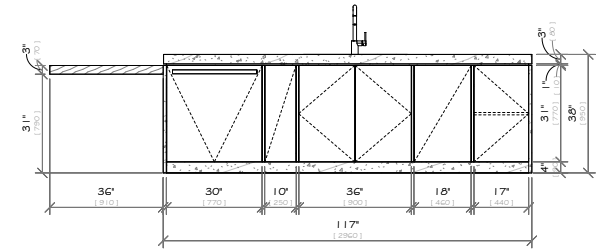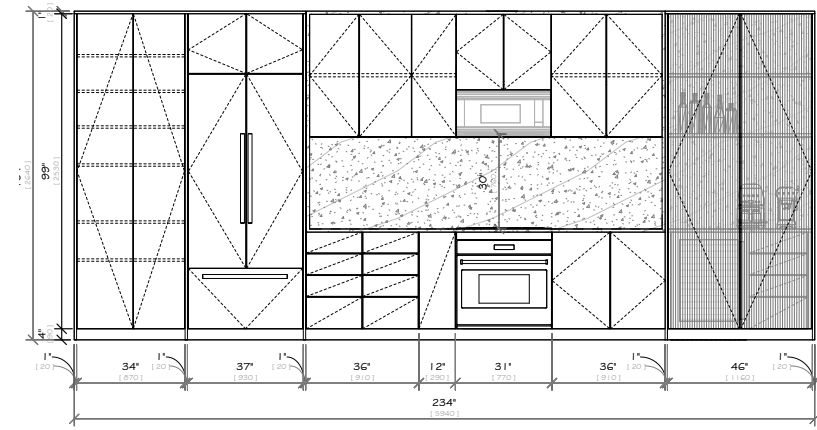

NOTE: UNDERCABINET LED STRIP LIGHTS FOR FIX SHELVINGS

PANTRY W/
ADJUSTABLE
SHELVES

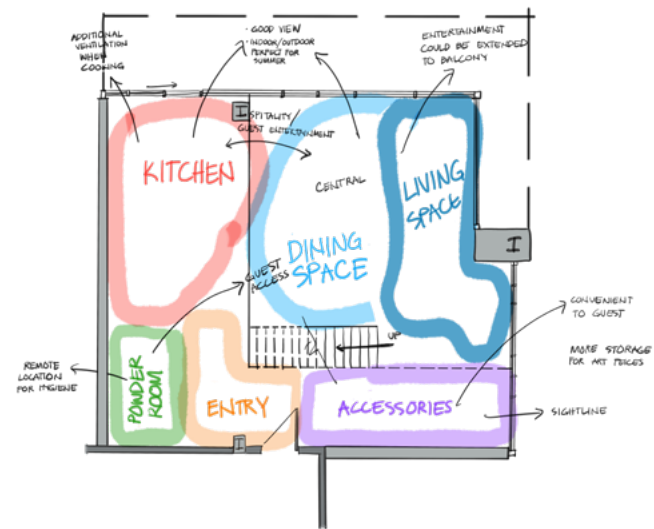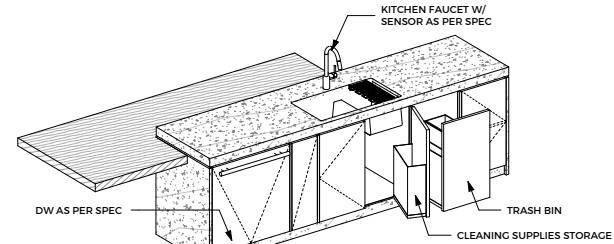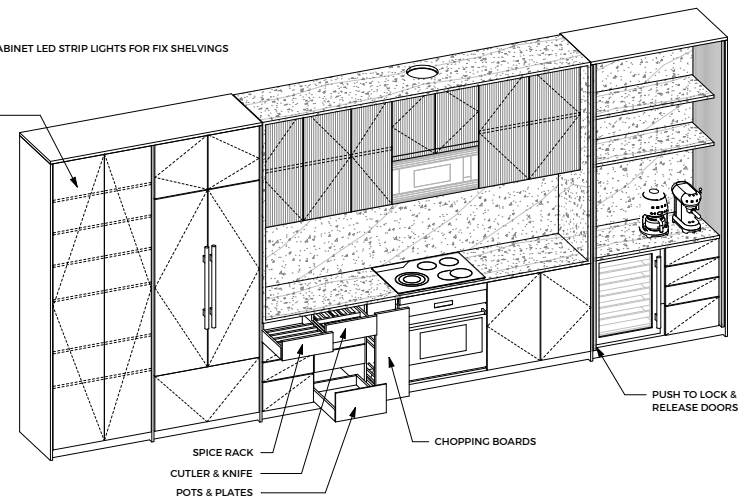

INDIGENOUS ARTTAKEN FROM COASTAL PEOPLES FINE ARTS GALLERY





2023 METAVERSE PHASE 1:

DIGITAL TWIN OF BARRETT CTI

VIRTUAL REALITY + GAMING + BRANDING

CONCEPT: THE PORTAL

NATURAL ELEMENTS + LIGHT | FLOOR SCULPTURE INSTALLATION



The Search of the Glow: Art Installation by Ling-Li Tseng



Arc Zero - Nimbus BY James Tapscott



Guiding Forms - Glass Prism Sculptures by Aurelie Abadie & Sauques Samuel

Humber College | Interior Design, Game Programming & Media Students

This phase focused on creating a **virtual replica** of the Barrett Centre for Technology Innovation to explore how the **metaverse** could be used for **education, design, and cross-program collaboration**. Students from **Interior Design, Game Programming, and Media Studies** worked together to build an interactive **3D environment** using **Revit, Twinmotion, and Unreal Engine**.

This phase demonstrates how interior design plays a key role in **multidisciplinary digital projects**, helping create virtual environments that are not only visually compelling but also intuitive and easy to navigate.


PORTAL FIBER OPTICS FIBER LIGHT INSTALLATION



<https://inspirationfeed.com/fiber-optic-installations-by-carlo-bernardini/>



FIBER OPTICS & METAL

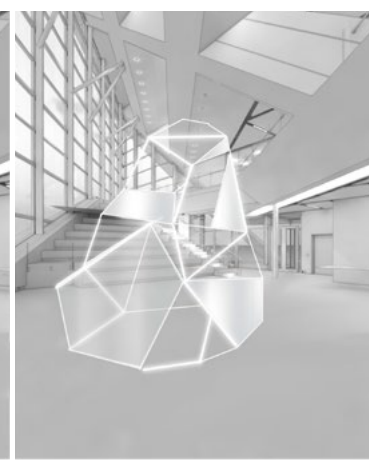

MIRROR, GLASS, FIBER OPTICS & METAL




BCTI BUILDING PORTAL INSTALLATION



VIRTUAL STAGE FILM VISUALIZATION STAGE



IMMERSSIVE MODE UNREAL ENGINE FOREST ENVIRONMENT

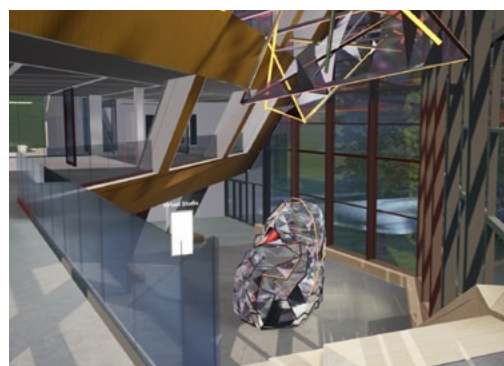

ME

PROJECT UPDATE

Default State

WHY SHOULD YOU READ THIS?

➔ Delve into a researcher's journey exploring the metaverse and its scope in education.

USING THE METAVERSE TO INNOVATE IN VIRTUAL PRODUCTION AND ARCHITECTURAL EDUCATION

BY JANICE SAJI

AT THE OFFICE OF RESEARCH & INNOVATION AT HUMBER COLLEGE, we often come across various curious minds interested in conducting research. Sometimes we come across faculty who have burning research questions that stem from a professional and educational background that enabled them to think about how to innovate in their field. They ask, "How can I combine all the amazing resources at Humber and formulate a robust research project with a diverse and talented team?"

Our response: We are here for you to realize your vision. ➔

2023

METaverse PHASE 2:

VIRTUAL PRODUCTION & INTERACTIVE TOOLS

VIRTUAL REALITY + ACADEMIC GAMING + BRANDING + UX/UI + WEBSITE DESIGN

SPARK

HUMBER'S RESEARCH & INNOVATION MAGAZINE | ISSUE #8 | OCTOBER 2023

DR. EVA ZIEMSEN AND ELIZABETH FENUTA ON

USING THE METAVERSE TO INNOVATE IN VIRTUAL PRODUCTION AND ARCHITECTURAL EDUCATION*

SotL Project Highlights

Humber's StoryLab Data Driven 2023 Coverage

Latest Updates on Innovative Research Projects

...and more!

HUMBER

Research & Innovation

HUMBER

PRESS

*We acknowledge the support of the Natural Sciences and Engineering Research Council of Canada (NSERC). Nous remercions le Conseil de recherches en sciences naturelles et en génie du Canada (CRSNG) de son soutien.

NSERC

CRSNG

MEET THE RESEARCH TEAM

Dr. Eva Ziemsen, Ph.D., is a professor in the Faculty of Media & Creative Arts at Humber College. She is a researcher, educator, and filmmaker with 20 years of experience. She holds a Ph.D. from the University of British Columbia, an MA in Feature Film Development and a Micro-Credential in Virtual Production completed at SIRT Centre. Dr. Ziemsen teaches courses in Virtual Production and is the lead curriculum developer of new programs in VP at Humber College. Dr. Ziemsen is an early adopter of Virtual Production and Metaverse technology; she has made films in virtual worlds and has taught in the Metaverse.

Elizabeth Fenuta is a professor of Architectural Technology in the Faculty of Applied Sciences & Technology (FAST) at Humber College and a licensed Architect. She received her Master of Architecture and Honors Bachelor of Architectural Studies from the University of Waterloo. Through the study of architecture in Italy and by working at various prestigious architecture and design firms in Toronto, she provides a unique interdisciplinary approach to spatial practice. Fenuta has taught at the University of Waterloo and researched with Dr. Elizabeth English on Amphibious Architectures. She has also taught Architecture at Toronto Metropolitan University and Interior Design at Yorkville University.

Speaking about the two research assistants who were part of the project, Dr. Ziemsen says, "Elizabeth and I are very focused on ensuring women are part of building the Metaverse and wish to amplify the complex technical work that these research assistants did."

EDUCATIONAL

LED VOLUME WALK-THROUGH

ELIJAH ALEJANDRO, FOURTH-YEAR INTERIOR DESIGN STUDENT AT HUMBER COLLEGE

Elijah Alejandro, a fourth-year Interior Design Student at Humber, and Ju-Chieh Liao, a graduate of Humber's Game Programming program, were the research assistants on this project.

Speaking about their experience working on the project, they said:

"I learned a lot while working on this project. This was my first time developing a VR application implementing interactive features and exploring text-to-speech technology. The highlight of this project was working together with team members from different fields and learning new things from them."

- JU-CHIEH LIAO, GRADUATE OF HUMBER'S GAME PROGRAMMING PROGRAM

"The project exposed me to new and different possibilities of Interior Design within the industry. It also honed me to improve other skills such as graphic design and web design."

- ELIJAH ALEJANDRO, FOURTH-YEAR INTERIOR DESIGN STUDENT AT HUMBER COLLEGE

The research assistants noted that this project served as valuable experience for their future careers.

"I gained valuable knowledge about Unreal Engine in implementing interactive features, optimizing performance, and creating video clips through a sequencer recorder which is an Unreal tool that I rarely use as a programmer. All these techniques enhance my knowledge of Unreal Engine while providing me the opportunity to understand the world of virtual production and metaverse."

- JU-CHIEH LIAO, GRADUATE OF HUMBER'S GAME PROGRAMMING PROGRAM

"Aside from learning technical skills and knowledge, Eva and Elizabeth have also empowered me to communicate my ideas and make them even better. These skills are very important especially when working towards a creative industry."

- ELIJAH ALEJANDRO, FOURTH-YEAR INTERIOR DESIGN STUDENT AT HUMBER COLLEGE

4 DR. EVA ZIEMSEN ALONG WITH HER RESEARCH ASSISTANTS, JU-CHIEH LIAO AND ELIJAH ALEJANDRO, AS THEY DEMO THEIR APP.

PROJECT UPDATE

PHOTOS BY CAMERON ROLLINS

PROJECT UPDATE

LED Tile

Custom designed LED specifically for the Film, Production and Broadcast industries. With a focus on exceptional on camera performance for Virtual Production, XR, AR, camera tracking shooting and video playback.

HUMBER METAVERSE

APG MEDIA

PROJECT OVERVIEW

Metaverse-Based Virtual Simulations for Virtual Production and Customer Engagement, Education and Training

A partnership between APG Media Group and Humber College on an Applied Research and Technology Partnership (ARTP) grant, with the generous support of the Natural Sciences and Engineering Research Council of Canada (NSERC) has produced a prototype for APG Media Group. The project, "Metaverse-Based Virtual Simulations for Virtual Production and Customer Engagement, Education and Training" is a collaboration led by researchers Eva Ziemsen, Ph.D. and Elizabeth Fenuta from Humber College and Vice President of Virtual Production Service Solutions Tim Hatch, BA from APG Media Group.

VIDEO WALK-THROUGH

APG Media x Humber College - Virtu...

Watch on YouTube

THE EDUCATIONAL LED VOLUME WALK-THROUGH

The Educational LED Volume Walk-Through allows the user to experience being in a Volume used for virtual production no matter where they are in the world. This application can run on your PC or using any Quest (VR) headset (linked to the PC for VR mode using Quest Link) and enables you to feel immersed in the volume. An AI will explain the different areas of the Volume, including the Brain Bar, Motion Tracking System, the LED wall, individual LED tiles and electrical distribution. Any prospective client or educational institution interested in education about VP

APG MEDIA

EDUCATIONAL

VOLUME WALK-THROUGH

EDUCATIONAL

LED VOLUME WALK-THROUGH

HUMBER COLLEGE + APG MEDIA | FUNDED BY NSERC (NATURAL SCIENCES AND ENGINEERING RESEARCH COUNCIL OF CANADA)

IN PHASE 2, THE TEAM EXPANDED THE PROJECT TO FOCUS ON VIRTUAL PRODUCTION, CREATING TOOLS FOR FILM, MEDIA, AND DESIGN EDUCATION. THIS INCLUDED:

A walkable virtual LED studio guided by AI narration, showing how real-time production works

A customizable studio design tool, where users can adjust layouts and finishes in real time using a PC or VR headset

THIS PHASE DEMONSTRATED HOW INTERIOR DESIGN CAN SUPPORT EMERGING TECHNOLOGIES—BRIDGING THE GAP BETWEEN VIRTUAL TOOLS AND REAL-WORLD ENVIRONMENTS THROUGH **COLLABORATIVE, CROSS-DISCIPLINARY DESIGN THINKING.**

HUMBER METAVERSE

x

APG MEDIA

EDUCATIONAL & CUSTOM VP LED VOLUME

An immersive virtual production experience accessible on PC or in VR. Users can explore a full LED Volume with guided explanations of core systems, or preview a custom-designed Volume tailored to specific studio requirements.